

GENERAL

1.
- The contractor is responsible for verifying all site dimensions, conditions, and existing services prior to starting work. Any discrepancies must be reported to the designer immediately.
2.
- Do not scale drawings. Use written dimensions only. Confirm any missing or unclear information with the design team before proceeding.
3.
- Contractor is responsible for understanding all project drawings, specifications, and contract documents. Report any conflicts among documents prior to construction.
4.
- All work shall comply with applicable municipal, provincial, and national building codes, as well as current safety regulations.
5.
- The contractor must ensure all necessary permits and approvals are secured prior to commencing work, unless otherwise noted.
6.
- Contractor is solely responsible for job site safety, including implementing safety protocols and protecting workers, equipment, and the building from damage.
7.
- The contractor must review and coordinate shop drawings, including layouts, loads, deflection data, and dimensions, with other trades before fabrication or construction.
8.
- All rough openings for doors, windows, and equipment must be verified on-site with suppliers before framing. Coordinate framing dimensions with architectural and supplier requirements.
9.
- Coordinate appliance and equipment sizes before fabricating any built-in elements, such as millwork or cabinetry.
10.
- Ensure all new surfaces are properly prepared to receive specified finishes. Match finishes to existing conditions as required.
11.
- Contractor shall confirm structural layout and site elevations and report any conflicts or irregularities before continuing work.
12.
- All exposed structural steel, fasteners, lintels, and other metal items must be galvanized or coated for corrosion resistance, unless noted otherwise.
13.
- Seal all joints, gaps, and penetrations at ducts, beams, and piping in exposed areas to ensure airtightness and maintain fire separation where applicable.
14.
- Only tested and certified firestop systems are to be used for any penetrations through rated assemblies. Canadian-listed firestopping materials are required.
15.
- Provide appropriate separation between dissimilar materials (e.g., steel and aluminum) using approved protective coatings or isolators to avoid galvanic corrosion.
16.
- Contractor is responsible for utility connections and for ensuring that all systems (power, water, data, gas, etc.) are fully operational at turnover.
17.
- Contractors and subcontractors are required to review all documentation and coordinate their work to avoid conflicts. Any unclear instructions must be clarified with the designer.
18.
- Protect completed work from dust, damage, and moisture during the construction process. Clean and repair any damage before handover.
19.
- Use only VOC-compliant materials and coatings. Avoid paints containing lead or mercury. Prioritize low-emission materials for indoor applications.
20.
- All lumber in contact with the ground or exposed to weather must be pressure-treated and compliant with preservation standards.
21.
- Where concrete is exposed in finished areas, provide a Class 'A' smooth finish as specified.
22.
- Install fire-rated and acoustically sealed barriers at all required partitions. All rated assemblies must be sealed at joints and penetrations as per code.
23.
- Backing and supports shall be installed in walls for items such as wall-hung cabinets, vanities, handrails, plumbing fixtures, and similar.
24.
- Do not reproduce, reuse, or modify these drawings without written authorization. These documents remain the intellectual property of INHABIT and are intended solely for the project noted.
25.
- Dimensions are typically taken from face of structural components (CMU, framing, concrete, etc.) unless otherwise indicated.
26.
- Final installation of doors, windows, and mechanical/electrical components must be verified with shop drawings and manufacturer requirements before installation.
27.
- All materials and workmanship shall follow best industry practices, manufacturers' specifications, and warranty requirements.

Revision History

RevID	ChID	Change Name	Date
01.	S.A	REISSUED FOR PERMIT	26 NOV.2025
02.	S.A	REISSUED FOR PERMIT	12 DEC.2025



inHabit

Projects + Design

inHabitPD@gmail.com
Halifax, NS

SOI TRADE INC - WALID SALLAM

WAREHOUSE EXTENSION

9 ALICIA SCOTT AVE.
MOUNT UNIACKE, NS
Canada
B0N 1Z0

Drawing Name

Drawing Status

ISSUED FOR PERMIT

Modified by

SA

Date

Oct 23, 2025

Checked by

BC

Date


Oct 23, 2025

Drawing Scale

Layout ID

A.01.1

Revision

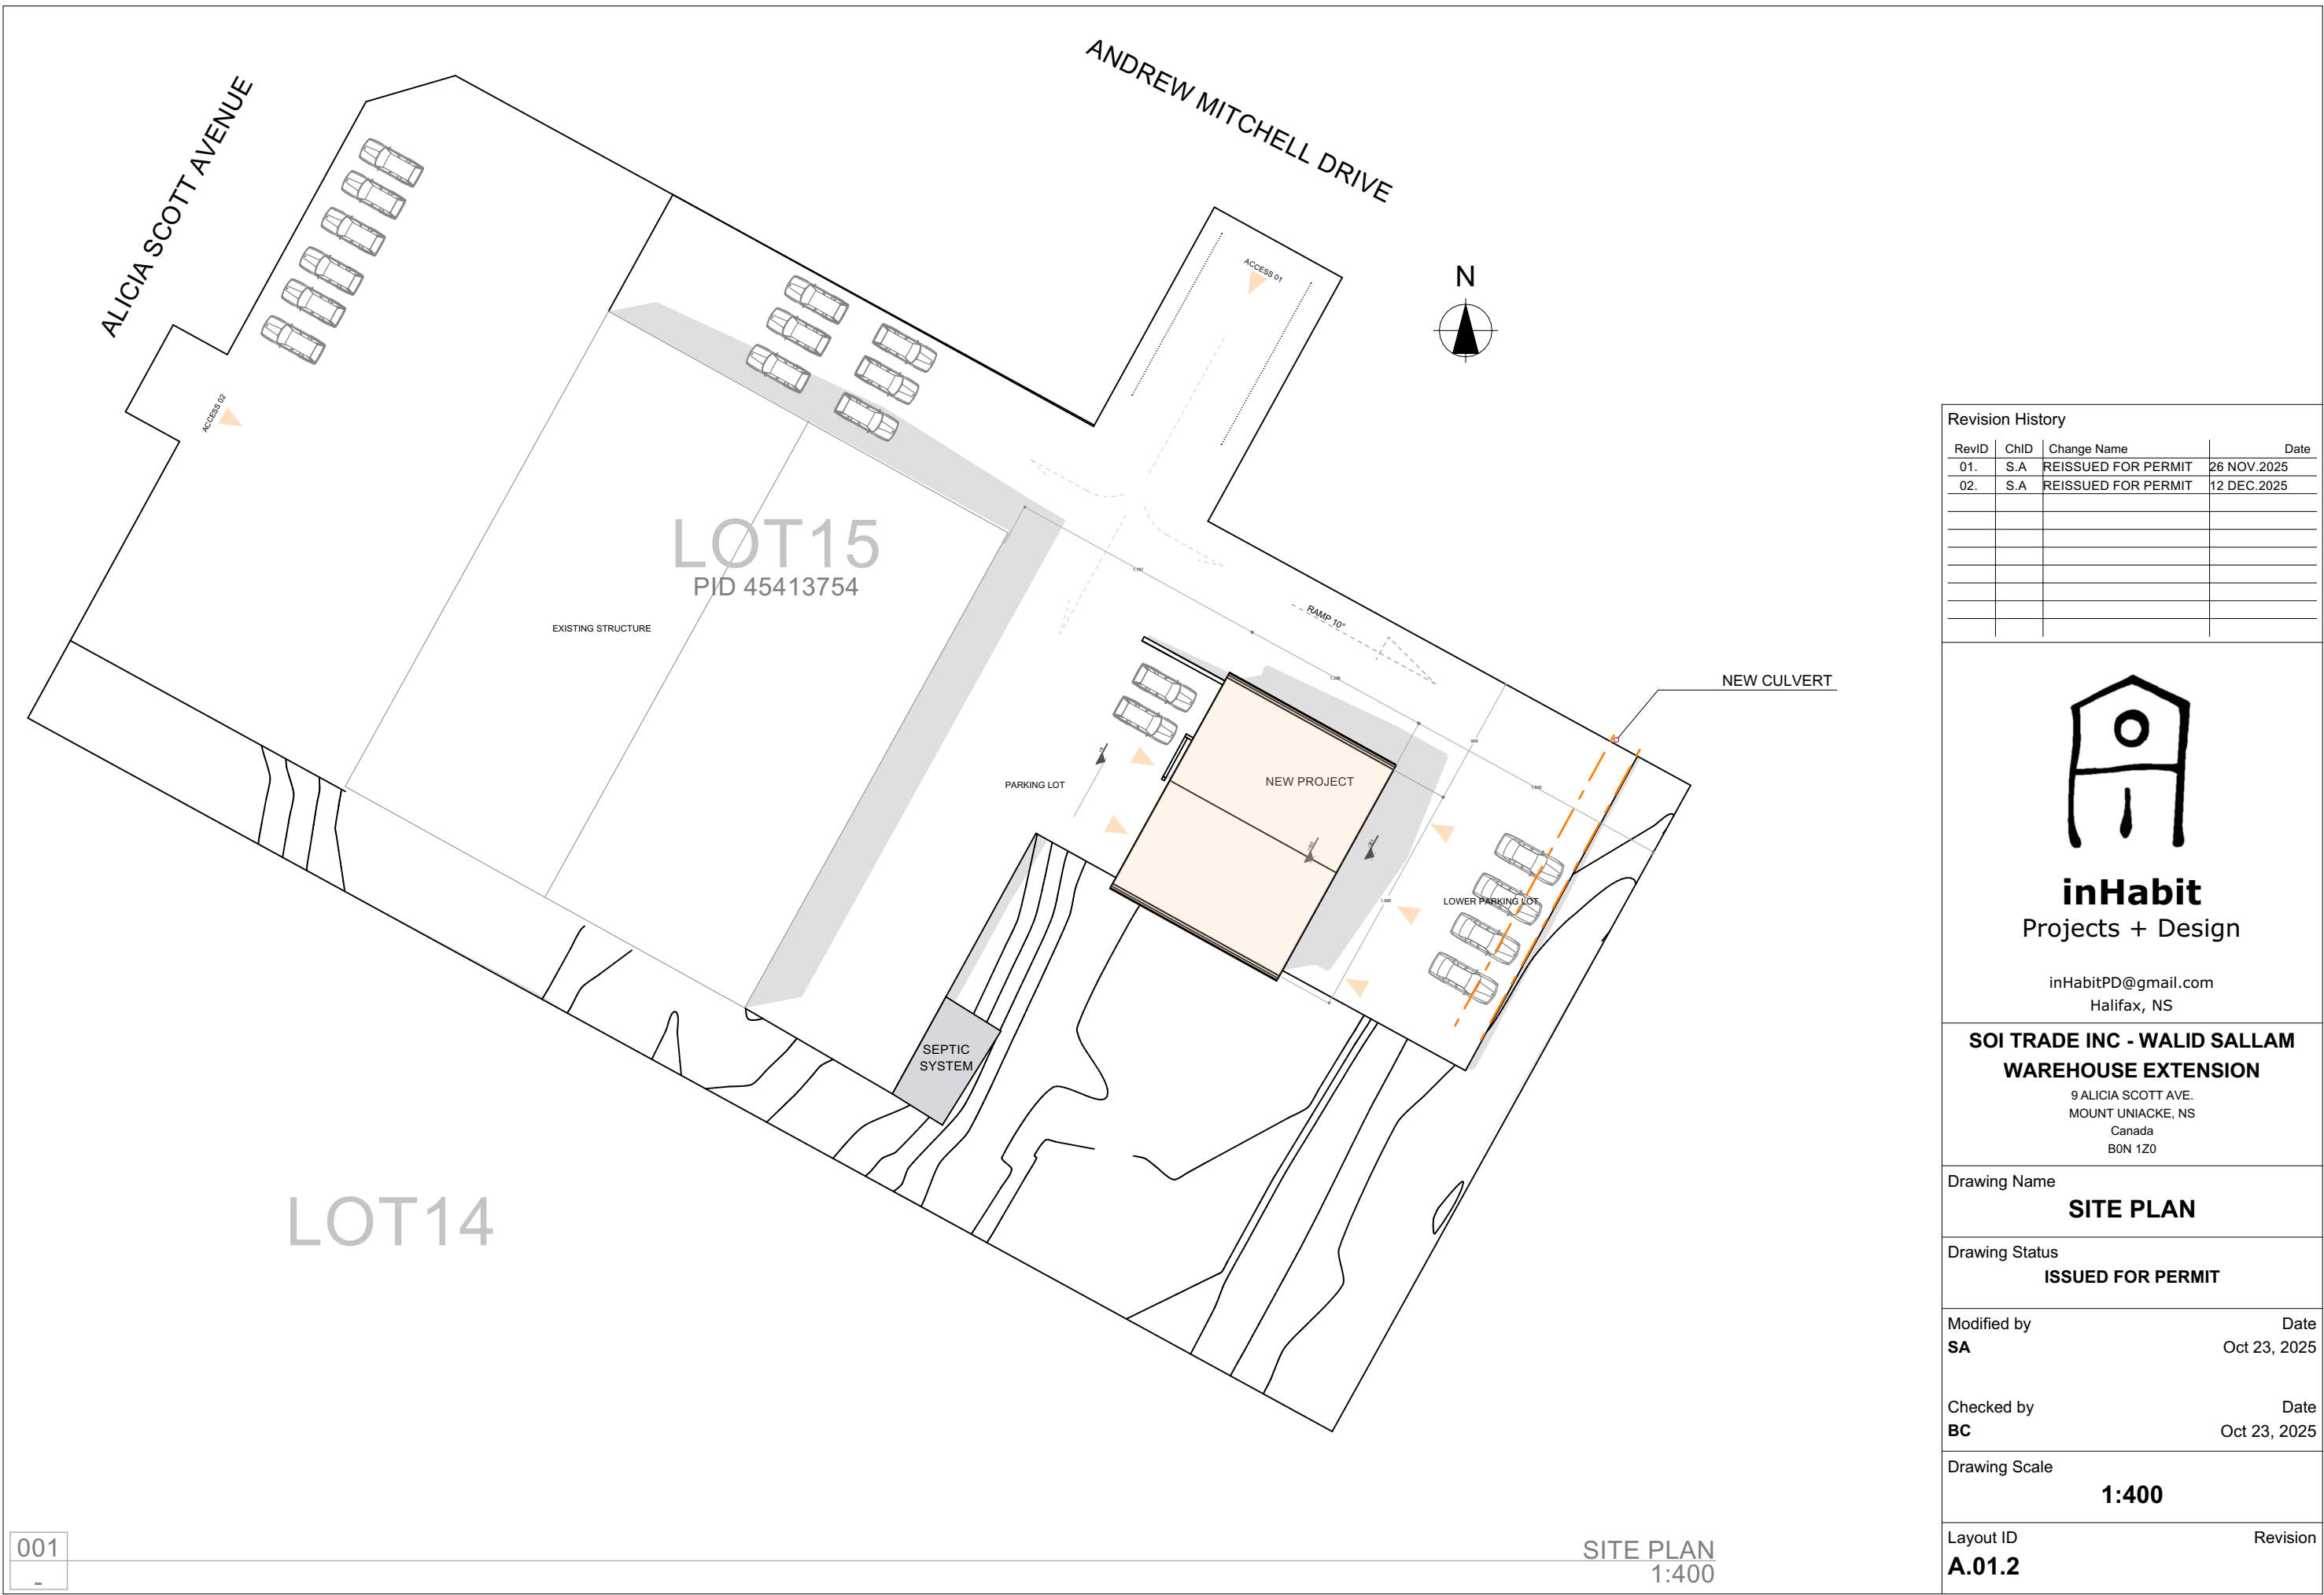

Revision History			
RevID	ChID	Change Name	Date
01.	S.A	REISSUED FOR PERMIT	26 NOV.2025
02.	S.A	REISSUED FOR PERMIT	12 DEC.2025



inHabit
Projects + Design

inHabitPD@gmail.com
Halifax, NS

SOI TRADE INC - WALID SALLAM
WAREHOUSE EXTENSION

9 ALICIA SCOTT AVE.
MOUNT UNIACKE, NS
Canada
B0N 1Z0

Drawing Name
SITE PLAN

Drawing Status
ISSUED FOR PERMIT

Modified by
SA

Date
Oct 23, 2025


Checked by
BC

Date
Oct 23, 2025


Drawing Scale
1:400

Layout ID
A.01.2

Revision

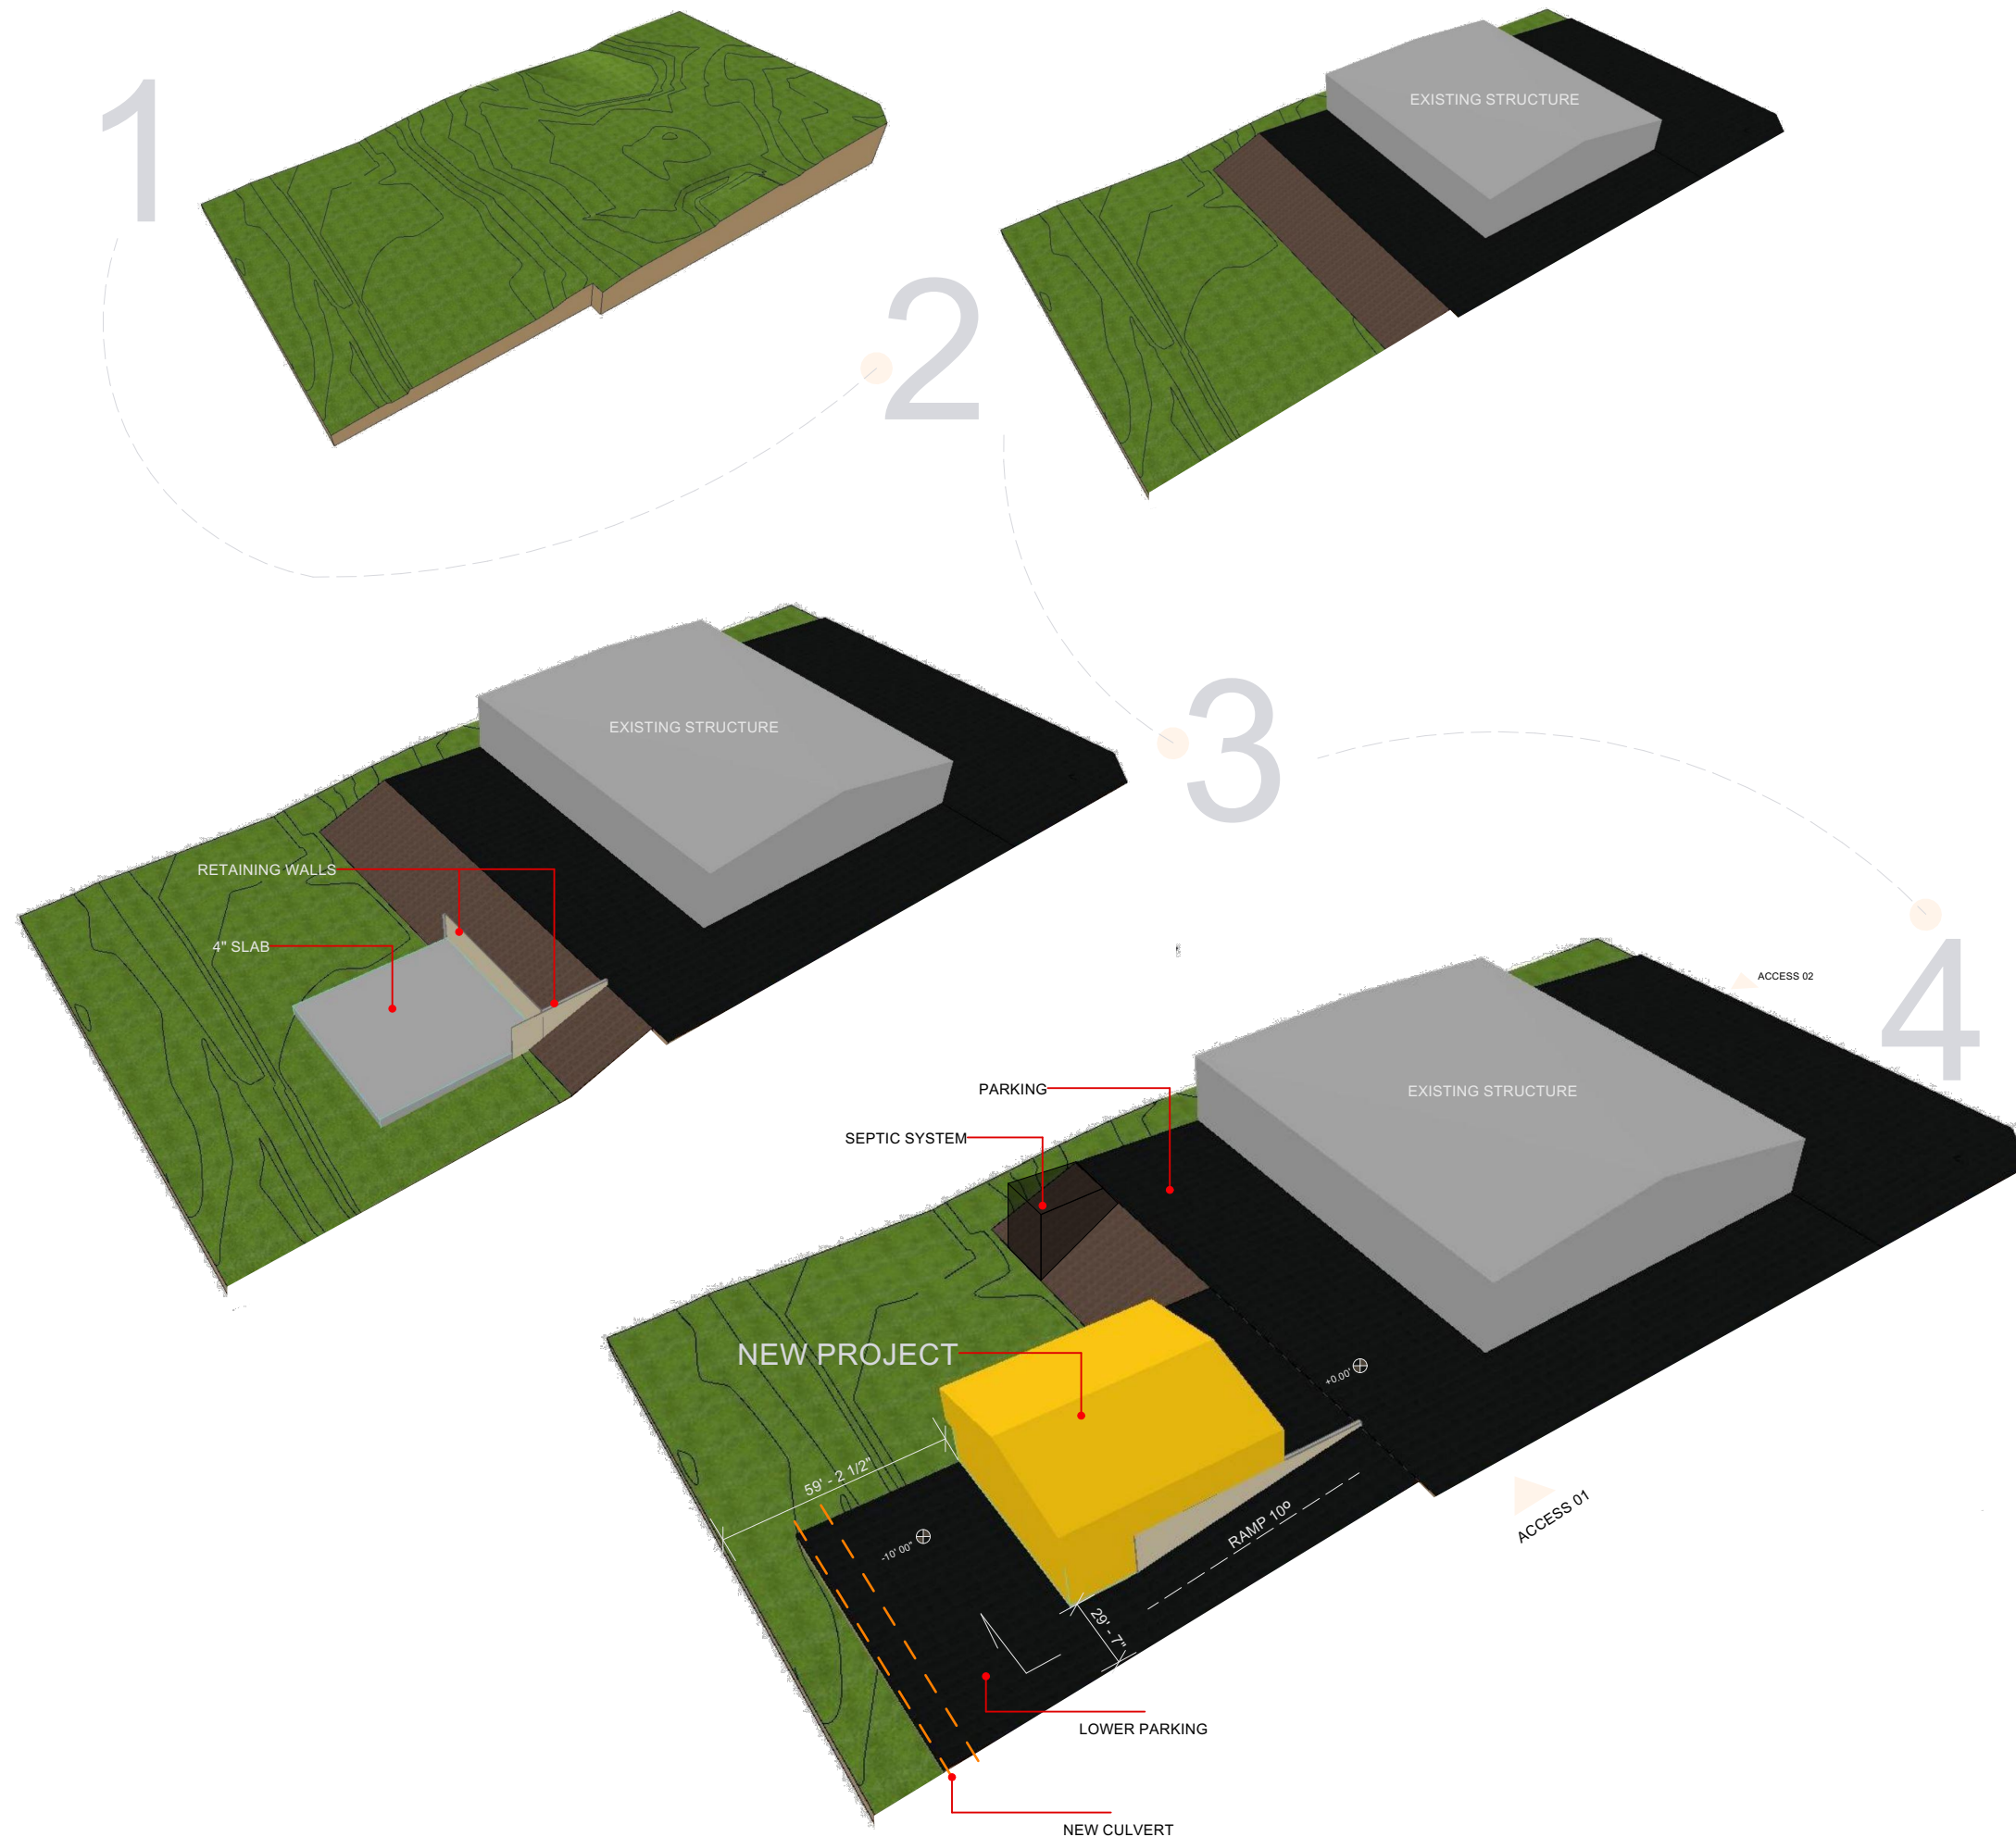

Revision History			
RevID	ChID	Change Name	Date
01.	S.A	REISSUED FOR PERMIT	26 NOV.2025
02.	S.A	REISSUED FOR PERMIT	12 DEC.2025

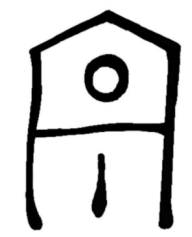

inHabit
Projects + Design

inHabitPD@gmail.com
Halifax, NS

SOI TRADE INC - WALID SALLAM
WAREHOUSE EXTENSION
9 ALICIA SCOTT AVE.
MOUNT UNIACKE, NS
Canada
B0N 1Z0

Drawing Name
SITE ANALYSIS

Drawing Status
ISSUED FOR PERMIT

Modified by
SA

Date
Oct 23, 2025

Checked by
BC


Date
Oct 23, 2025

Drawing Scale


Layout ID
A.01.3

Revision


EXTERIOR WALL ASSEMBLIES

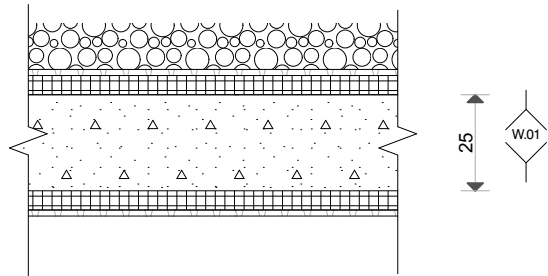


- FOUNDATION WALL (BELOW GRADE)**
- GRAVEL FILL
 - DRAINAGE MAT
 - 2" RIGID INSULATION
 - 10" FOUNDATION WALL -SEE STRUCTURAL-
 - 2" RIGID INSULATION

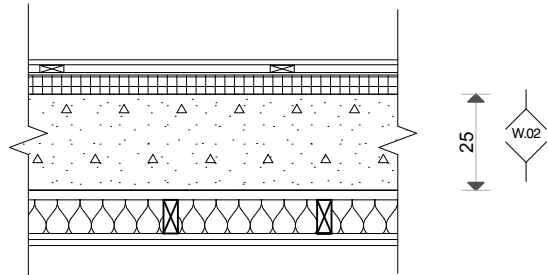


- FOUNDATION WALL (ABOVE GRADE)**
- EXTERIOR CLADDING OR SIDING
 - 1x3 STRAPPING @ 2' O.C.
 - AIR BARRIER MEMBRANE
 - 2" RIGID INSULATION
 - 10" CONCRETE WALL -SEE STRUCTURAL-
 - 1" AIR SPACE
 - 2x4 WOOD STUDS @ 16" O.C.
 - 3-1/2" BATT INSULATION
 - 6 mil. POLY VAPOUR BARRIER
 - 2x 5/8" GWB

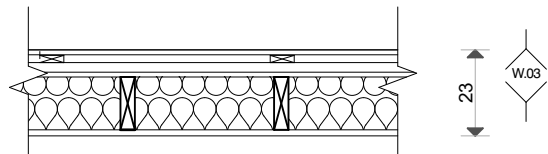

- EXTERIOR WOOD STUD WALL w/ CLADDING**
- EXTERIOR CLADDING OR SIDING
 - 1x3 STRAPPING @ 2' O.C.
 - AIR BARRIER MEMBRANE
 - 1" SEMI-RIGID MINERAL WOOL INSULATION
 - 1/2" PLYWOOD SHEATHING
 - 2x6 WOOD STUDS @ 16" O.C.
 - 5 1/2" MINERAL WOOL FIBRE INSULATION
 - 6 mil. POLY VAPOUR BARRIER
 - 5/8" TYPE-X GWB

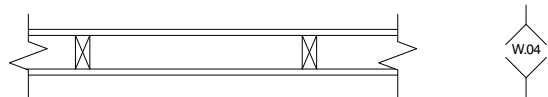


- INTERIOR PARTITION**
- 5/8" GWB
 - 2x4 WOOD STUDS @ 16" O.C.
 - 5/8" GWB

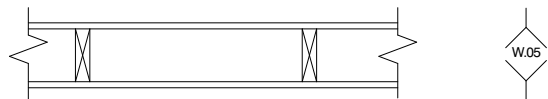


- INTERIOR PARTITION**
- 5/8" GWB
 - 2x6 WOOD STUDS @ 16" O.C.
 - 5/8" GWB

FLOOR ASSEMBLIES

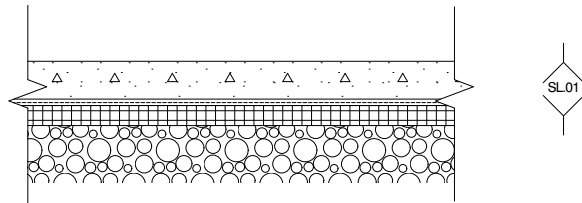


- SLAB ON GRADE**
- FINISH FLOORING
 - 5" CONCRETE SLAB ON GRADE
 - 6mil. VAPOR BARRIER PLASTIC SHEET
 - 2" RIGID INSULATION
 - MIN. 6" CRUSHED STONE

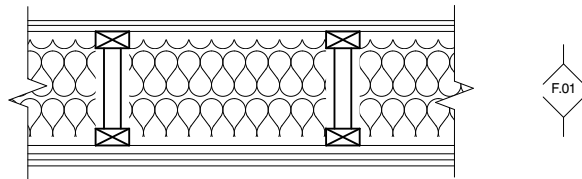

- FLOOR -ENGINEERED WOOD STRUCTURE**
- FINISH FLOORING
 - 5/8" PLYWOOD SUB-FLOOR LAYER
 - ENGINEERED WOOD FLOOR STRUCTURE
 - JOIST CAVITIES FILLED WITH MINERAL WOOL INSULATION
 - 1x3 STRAPPING @ 24" O.C.
 - 2x 5/8" TYPE-X GB

ROOF ASSEMBLIES

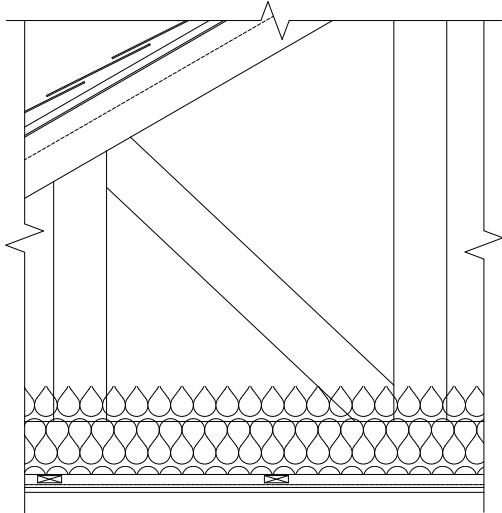

- ASPHALT SHINGLES
- ICE AND WATER SHIELD
- AIR BARRIER MEMBRANE
- 3/4" PLYWOOD ROOF SHEATHING
- PRE-ENGINEERED ROOF TRUSSES
- MIN. 10-1/2" BLOW-IN CELLULOSE INS. R35
- 1x3 WOOD STRAPPING @ 24" O.C.
- 6mil POLY VAPOUR BARRIER
- 5/8" CEILING GWB

Revision History			
RevID	ChID	Change Name	Date
01.	S.A	ISSUED FOR PERMIT	12 DEC.2025



inHabit
Projects + Design

inHabitPD@gmail.com
Halifax, NS

SOI TRADE INC - WALID SALLAM
WAREHOUSE EXTENSION

9 ALICIA SCOTT AVE.
MOUNT UNIACKE, NS
Canada
B0N 1Z0

Drawing Name
CONSTRUCTION ASSEMBLIES

Drawing Status
ISSUED FOR PERMIT

Modified by
SA

Date
Oct 23, 2025


Checked by
BC

Date
Oct 23, 2025

Drawing Scale
1:20

Layout ID
A.01.4

Revision

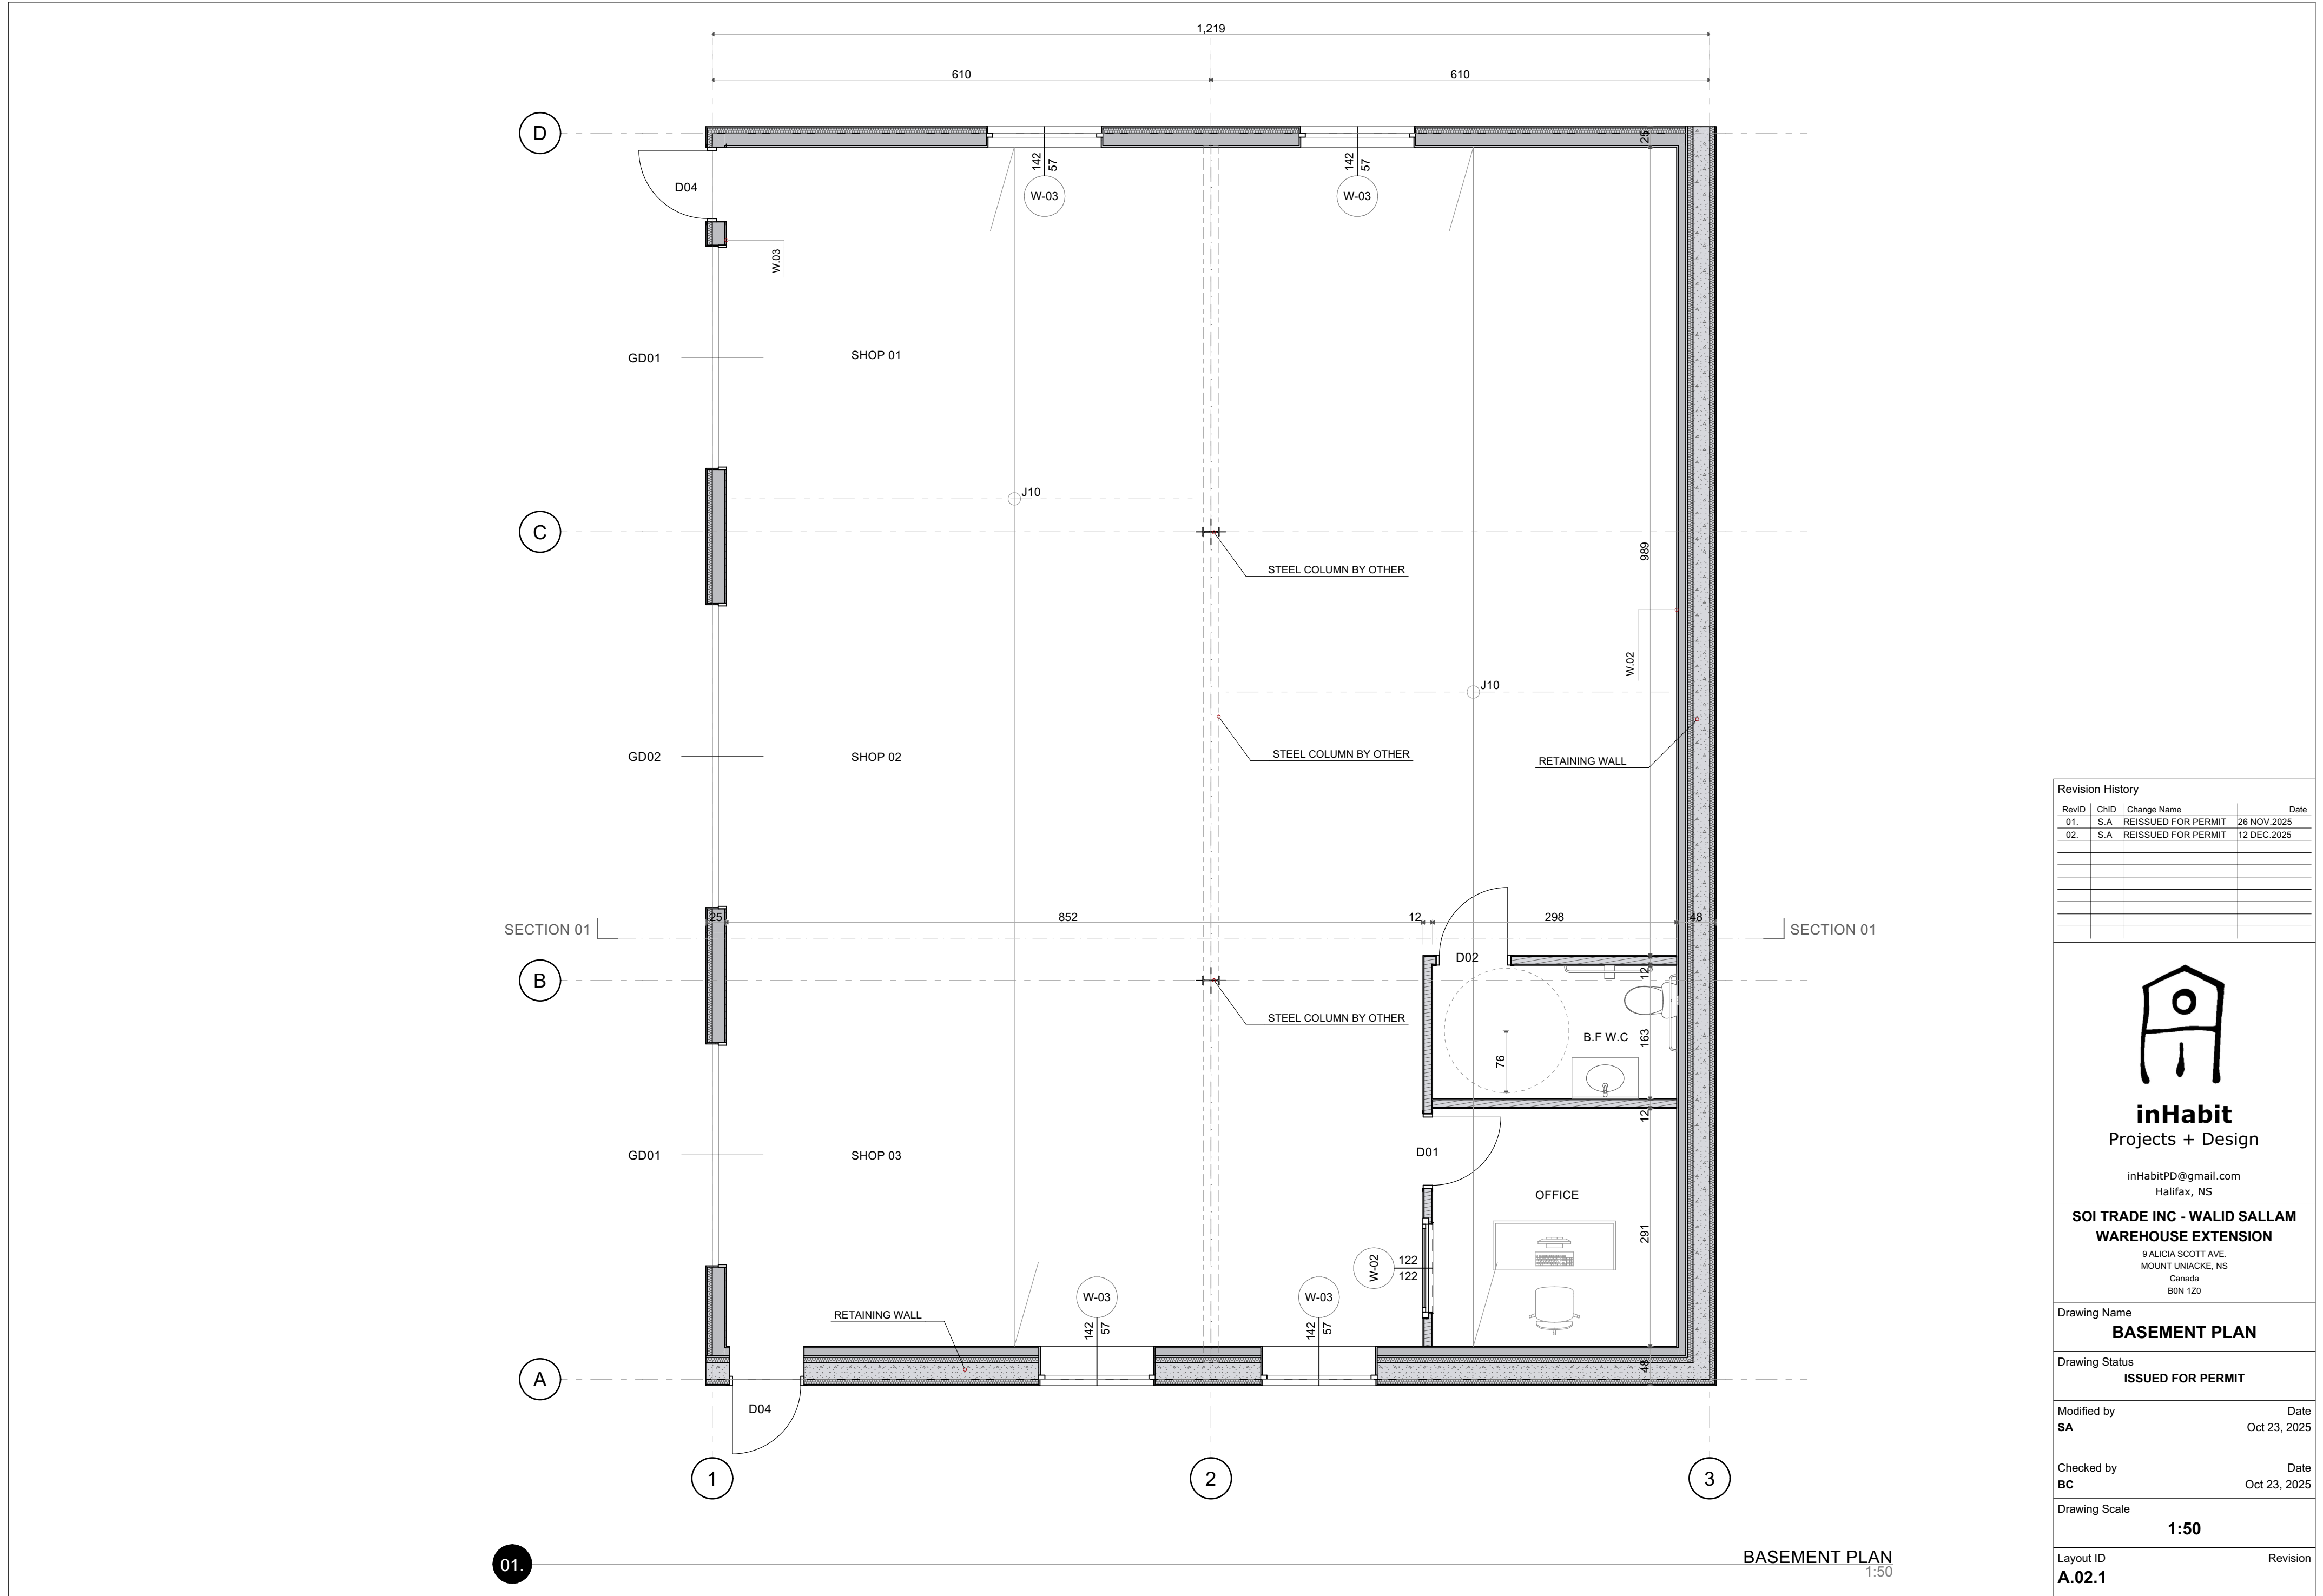

Revision History			
RevID	ChID	Change Name	Date
01.	S.A	REISSUED FOR PERMIT	26 NOV.2025
02.	S.A	REISSUED FOR PERMIT	12 DEC.2025



inHabit
Projects + Design

inHabitPD@gmail.com
Halifax, NS

SOI TRADE INC - WALID SALLAM
WAREHOUSE EXTENSION

9 ALICIA SCOTT AVE.
MOUNT UNIACKE, NS
Canada
B0N 1Z0

Drawing Name	
BASEMENT PLAN	
Drawing Status	
ISSUED FOR PERMIT	
Modified by	Date
SA	Oct 23, 2025
Checked by	Date
BC	Oct 23, 2025
Drawing Scale	
1:50	
Layout ID	Revision
A.02.1	



InHabit
Projects + Design

inHabitPD@gmail.com
Halifax, NS

inHabit
Projects + Design

Halifax, NS

SOI TRADE INC - WALID SALLAM
WAREHOUSE EXTENSION

9 ALICIA SCOTT AVE.
MOUNT UNIACKE, NS
Canada
B0N 1Z0

Drawing Name	Notes
1.00	
2.00	
GROUND LEVEL

Drawing Status

ISSUED FOR PERMIT

Modified by

SA

Date _____

Oct 23, 2025

Checked by

BC

Date _____

Oct 23, 2025


Drawing Scale

1:50


Layout ID

A.02.2

Revision

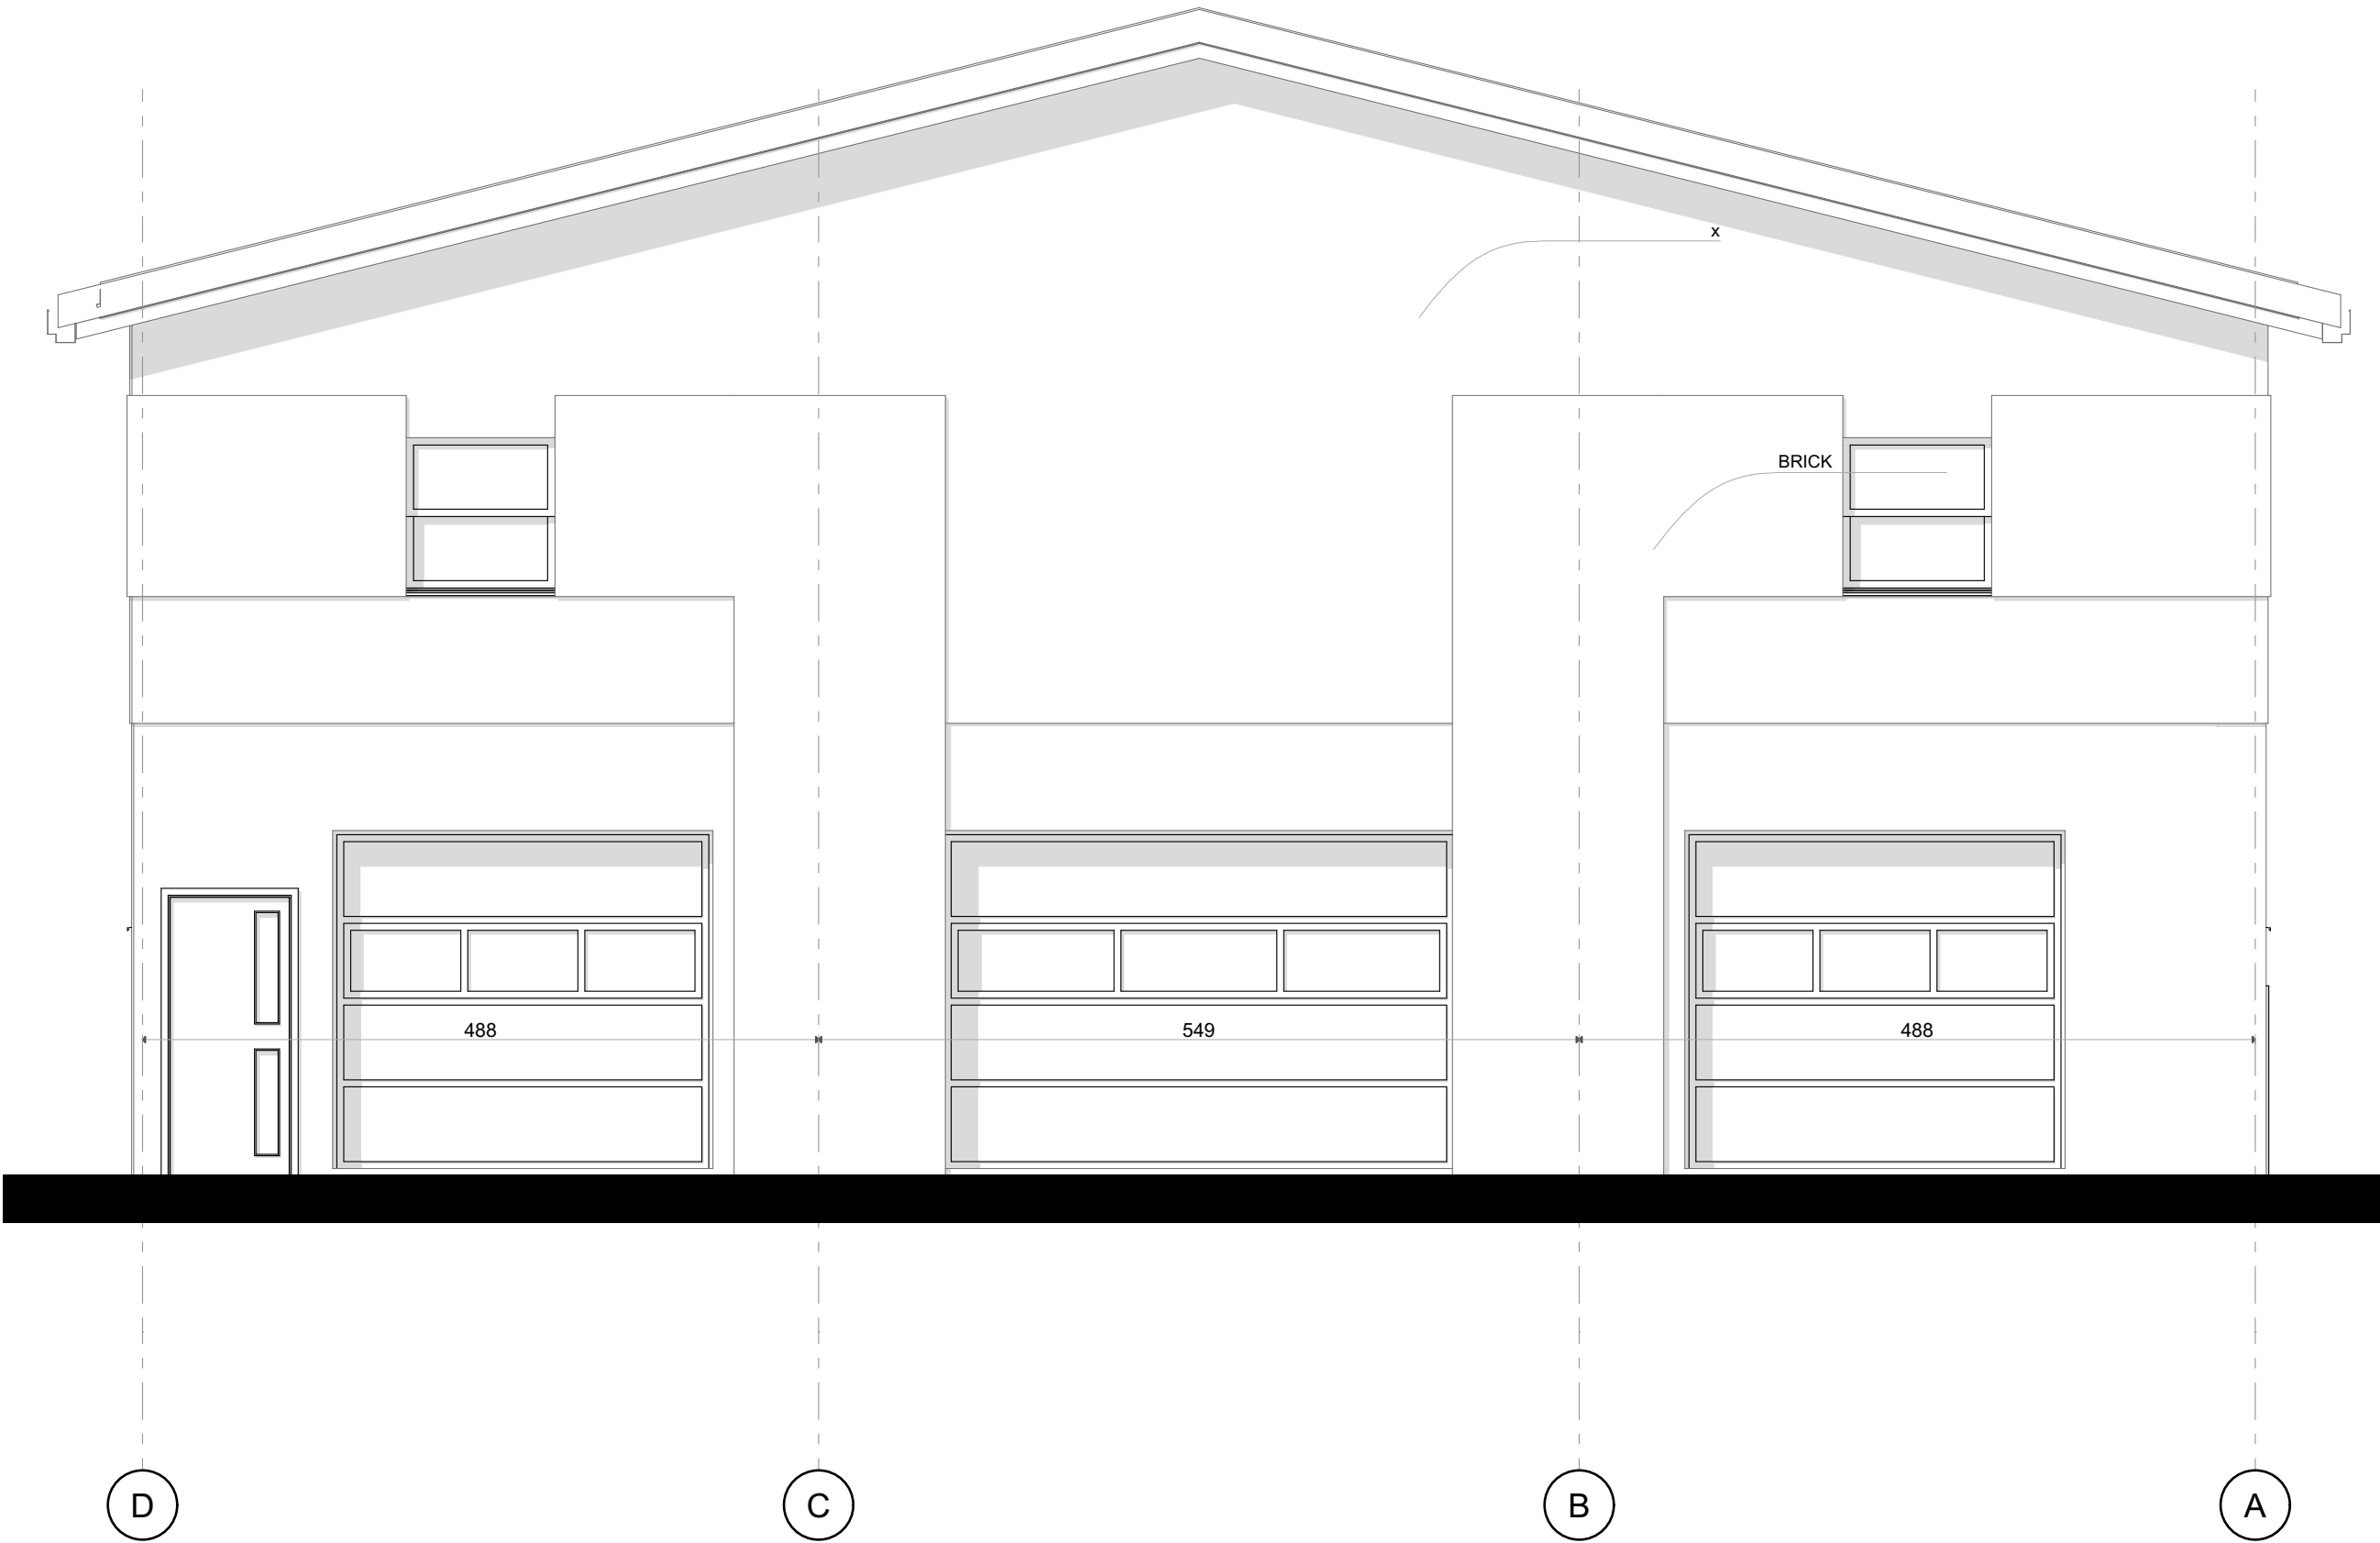

Revision History			
RevID	ChID	Change Name	Date
01.	S.A	ISSUED FOR PERMIT	12 DEC.2025

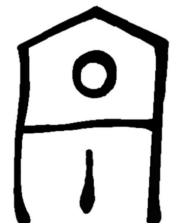

inHabit
Projects + Design

inHabitPD@gmail.com
Halifax, NS

SOI TRADE INC - WALID SALLAM
WAREHOUSE EXTENSION
9 ALICIA SCOTT AVE.
MOUNT UNIACKE, NS
Canada
B0N 1Z0

Drawing Name
ELEVATION BACK

Drawing Status
ISSUED FOR PERMIT

Modified by
SA

Date
Oct 23, 2025

Checked by
BC

Date
Oct 23, 2025

Drawing Scale
1:50

Layout ID
A.03.1

Revision



A

B

C

D

ELEVATION FACE

1:50

Revision History			
RevID	ChID	Change Name	Date
01.	S.A	ISSUED FOR PERMIT	12 DEC.2025



inHabit
Projects + Design

inHabitPD@gmail.com
Halifax, NS

SOI TRADE INC - WALID SALLAM
WAREHOUSE EXTENSION

9 ALICIA SCOTT AVE.
MOUNT UNIACKE, NS
Canada
B0N 1Z0

Drawing Name

ELEVATION FACE

Drawing Status

ISSUED FOR PERMIT


Modified by	Date
SA	Oct 23, 2025

Checked by	Date
BC	Oct 23, 2025

Drawing Scale

1:50

Layout ID	Revision
A.03.2	

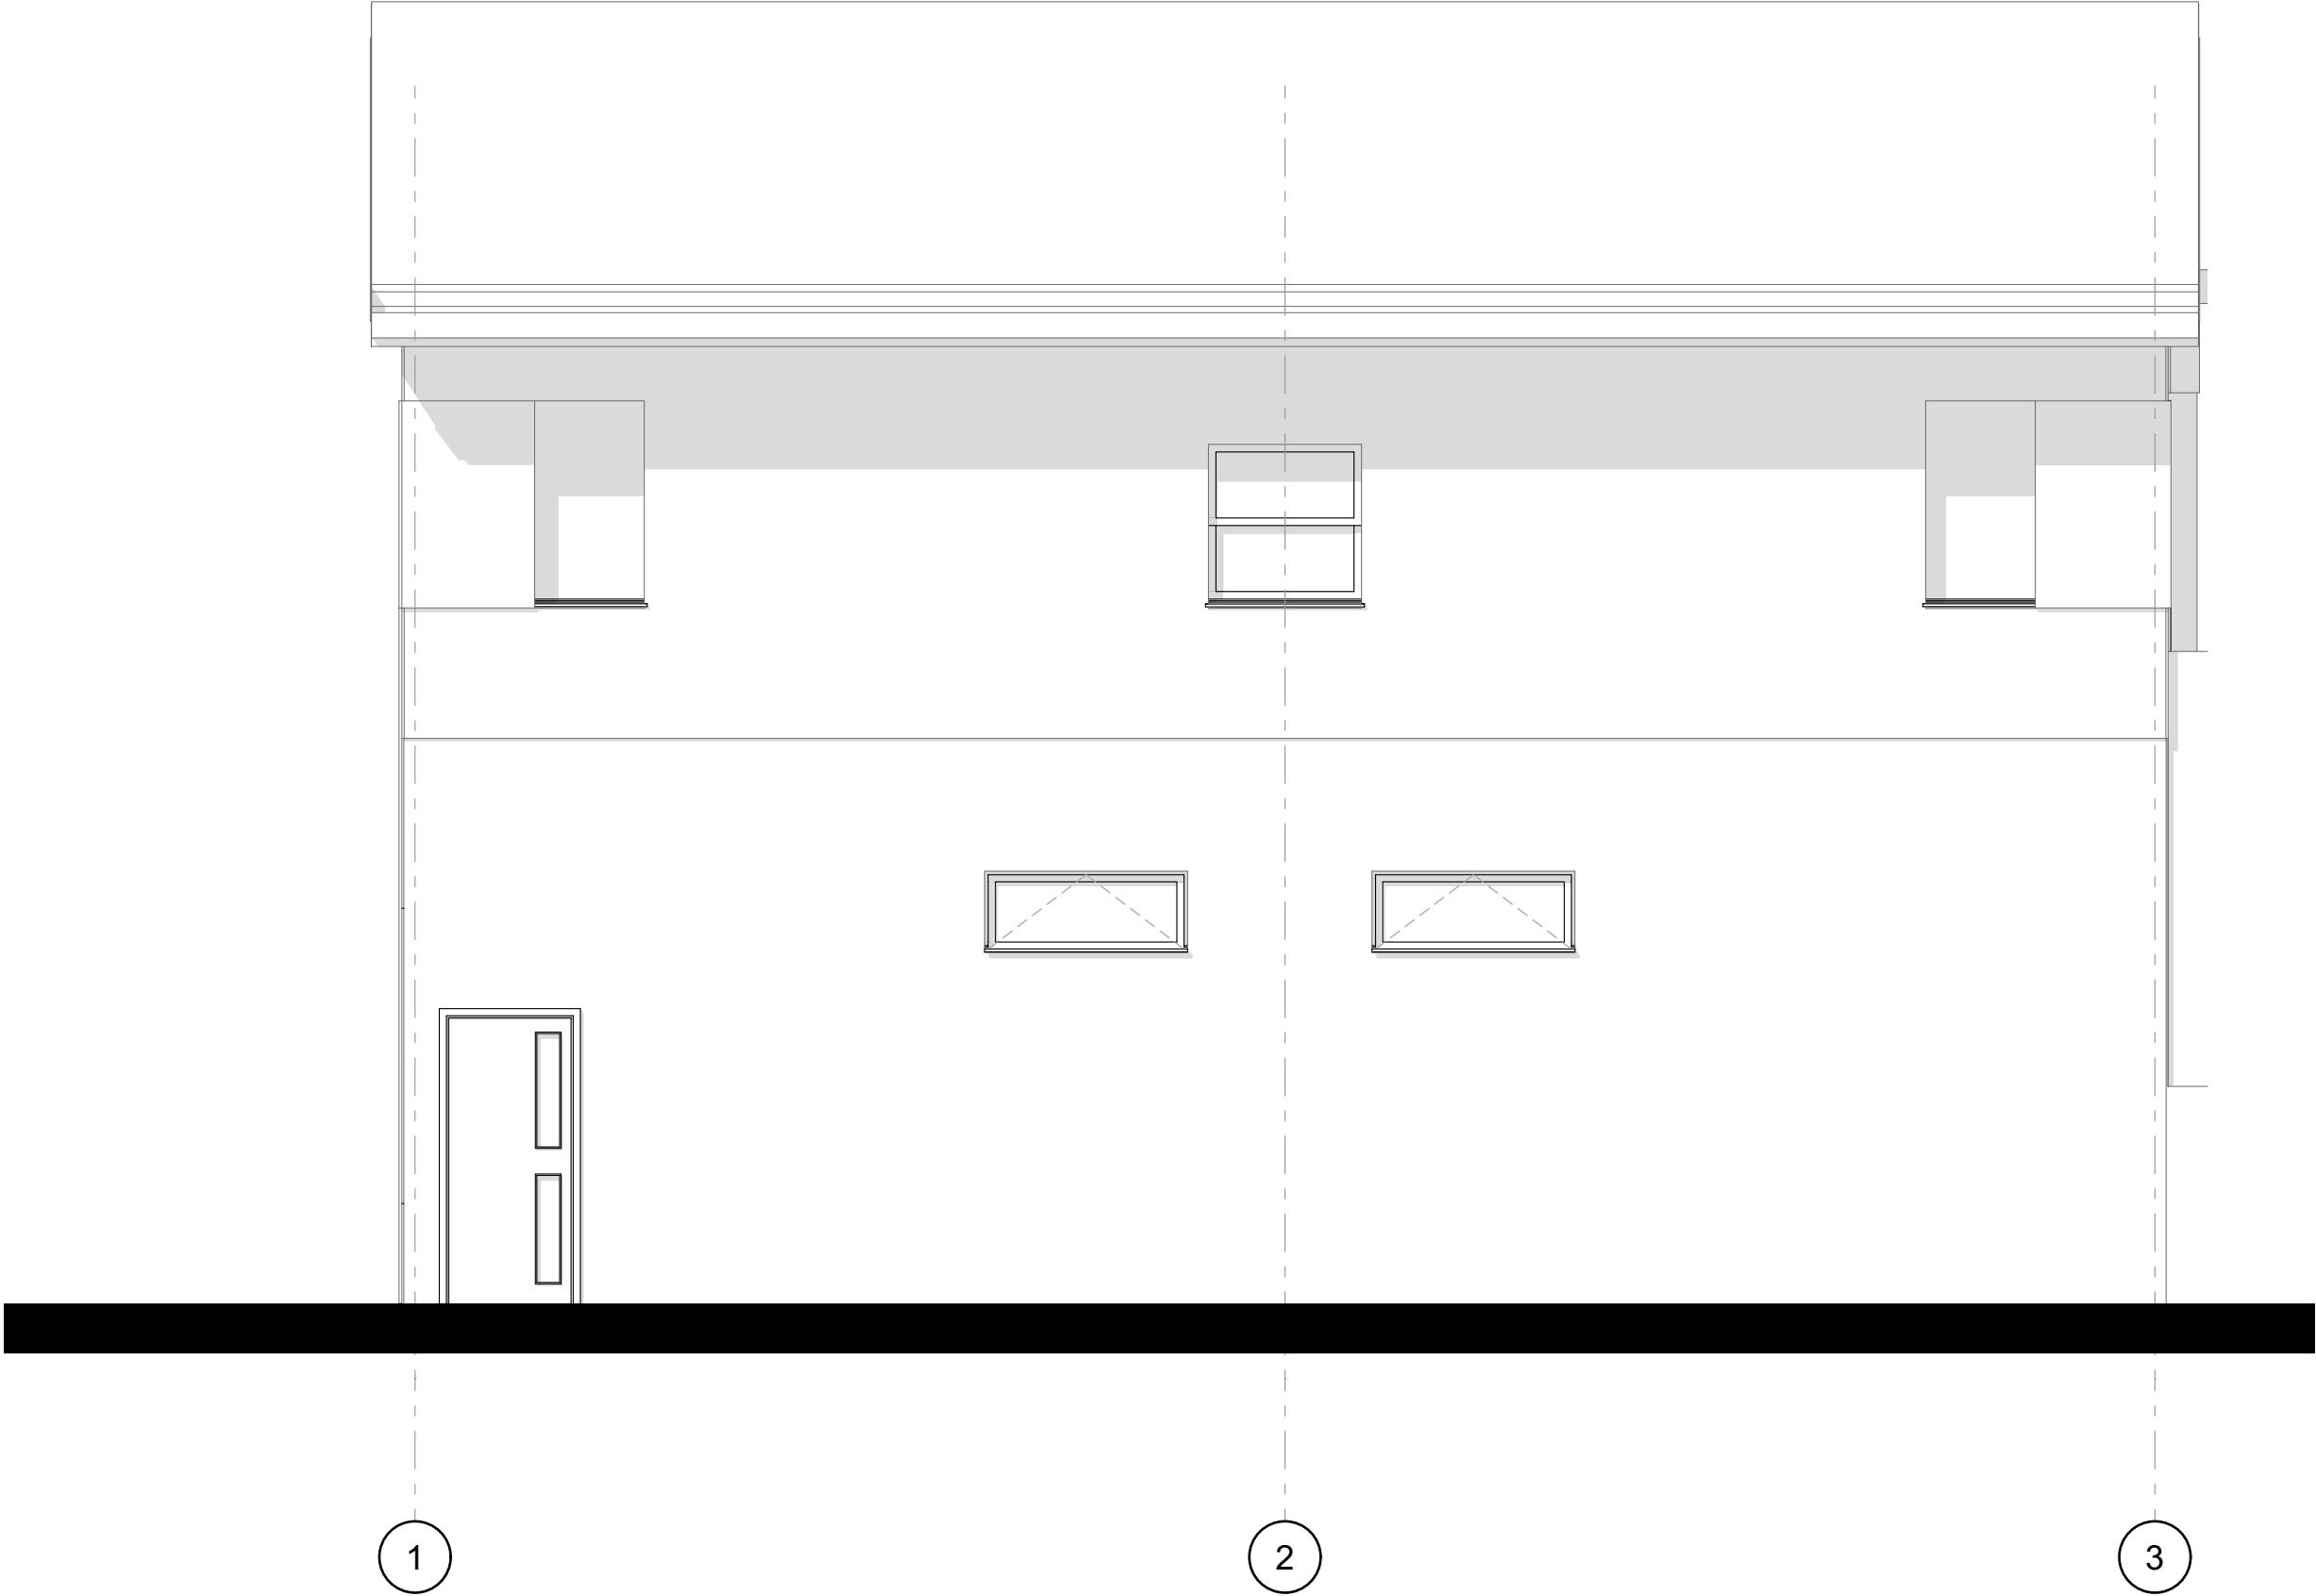

ELEVATION LEFT

1:50

Revision History			
RevID	ChID	Change Name	Date
01.	S.A	ISSUED FOR PERMIT	12 DEC.2025



inHabit
Projects + Design

inHabitPD@gmail.com
Halifax, NS

SOI TRADE INC - WALID SALLAM
WAREHOUSE EXTENSION
9 ALICIA SCOTT AVE.
MOUNT UNIACKE, NS
Canada
B0N 1Z0

Drawing Name
ELEVATION LEFT


Drawing Status
ISSUED FOR PERMIT

Modified by	Date
SA	Oct 23, 2025


Checked by	Date
BC	Oct 23, 2025

Drawing Scale
1:50

Layout ID	Revision
A.03.3	

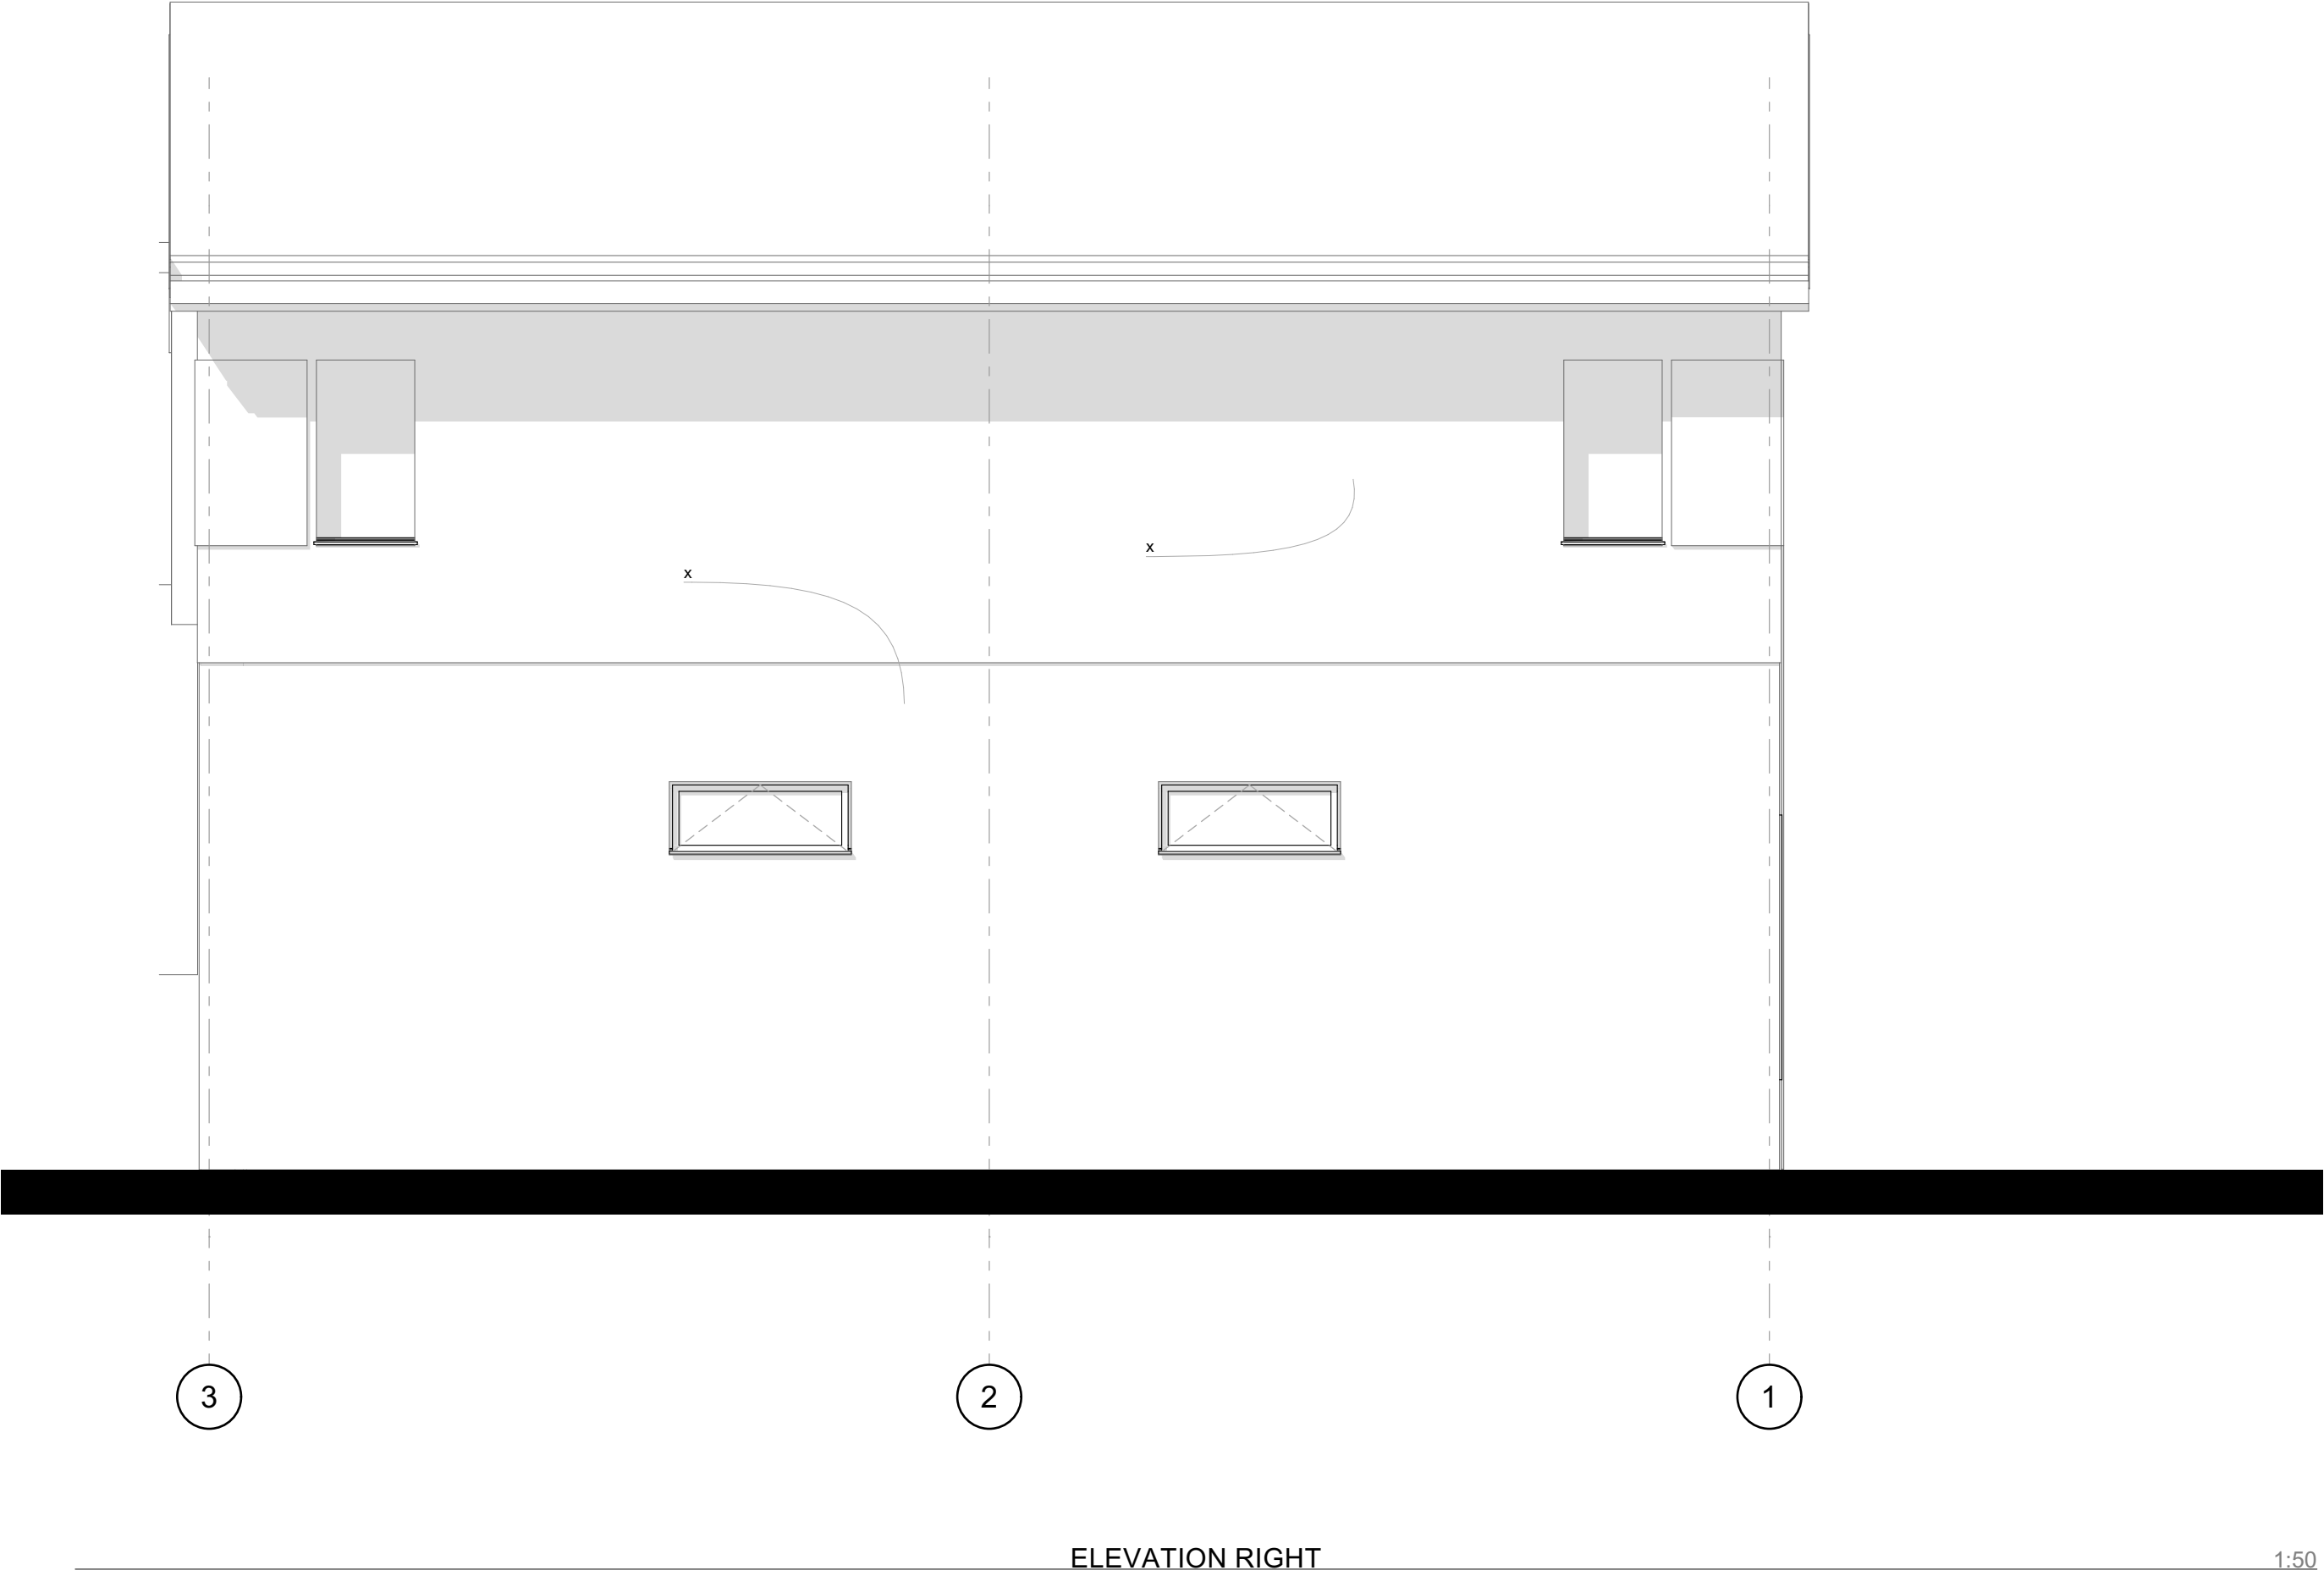

Revision History			
RevID	ChID	Change Name	Date
01.	S.A	ISSUED FOR PERMIT	12 DEC.2025

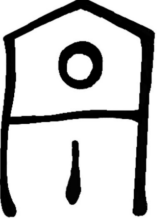

inHabit
Projects + Design

inHabitPD@gmail.com
Halifax, NS

SOI TRADE INC - WALID SALLAM
WAREHOUSE EXTENSION
9 ALICIA SCOTT AVE.
MOUNT UNIACKE, NS
Canada
B0N 1Z0

Drawing Name
ELEVATION RIGHT


Drawing Status
ISSUED FOR PERMIT

Modified by	Date
SA	Oct 23, 2025

Checked by	Date
BC	Oct 23, 2025

Drawing Scale
1:50

Layout ID	Revision
A.03.4	

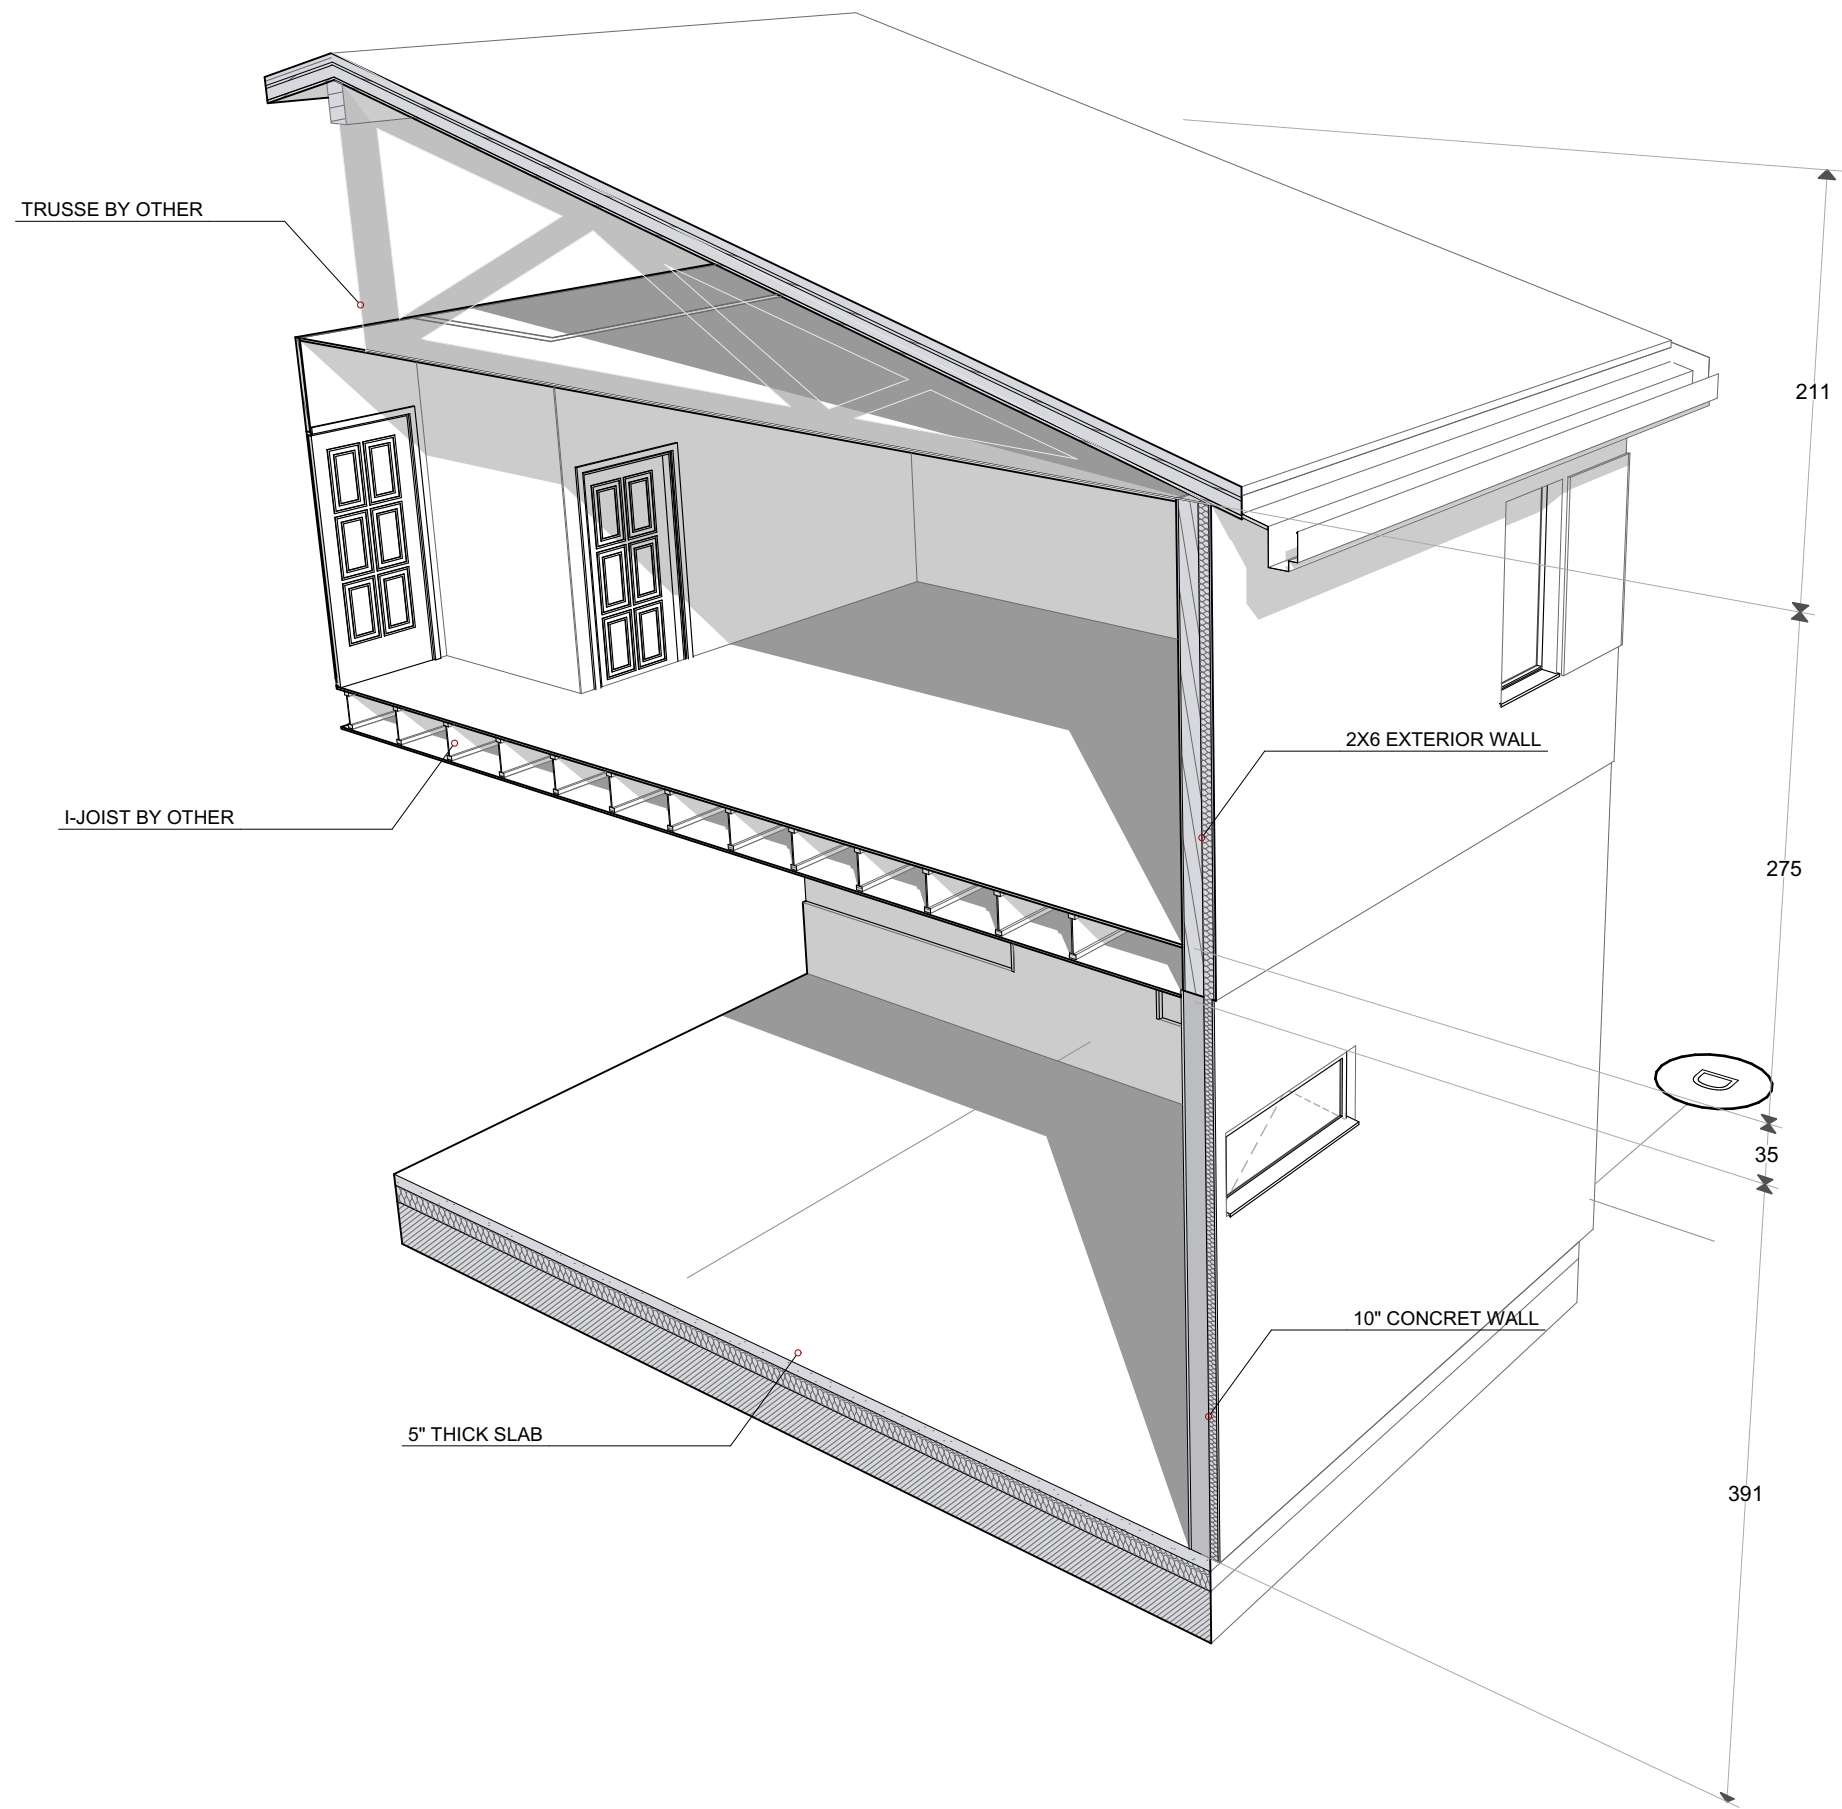

A04-01. 1- 3D SECTION

Revision History			
RevID	ChID	Change Name	Date
01.	S.A	ISSUED FOR PERMIT	12 DEC.2025



inHabit
Projects + Design

inHabitPD@gmail.com
Halifax, NS

SOI TRADE INC - WALID SALLAM
WAREHOUSE EXTENSION
9 ALICIA SCOTT AVE.
MOUNT UNIACKE, NS
Canada
B0N 1Z0

Drawing Name
3D SECTION


Drawing Status
ISSUED FOR PERMIT

Modified by	Date
SA	Oct 23, 2025


Checked by	Date
BC	Oct 23, 2025

Drawing Scale
1:100


Layout ID	Revision
A.04.1	

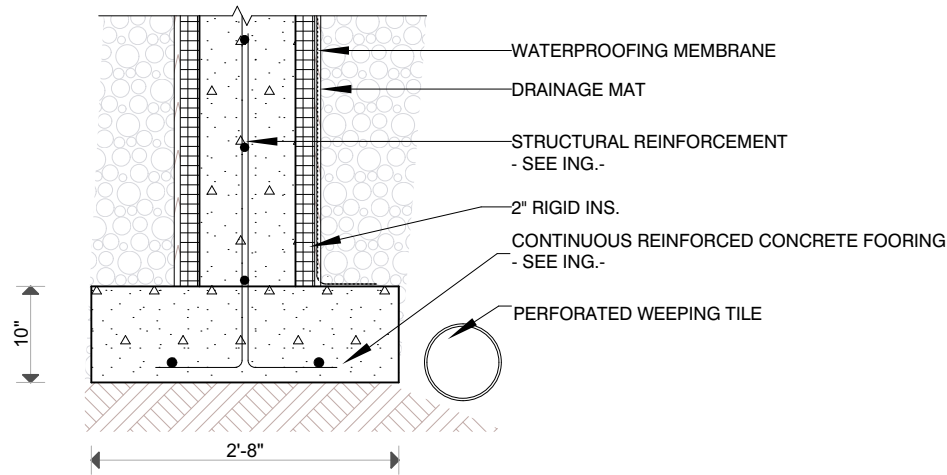


A04-02. 1- FOUNDATION FOOTING SECTION

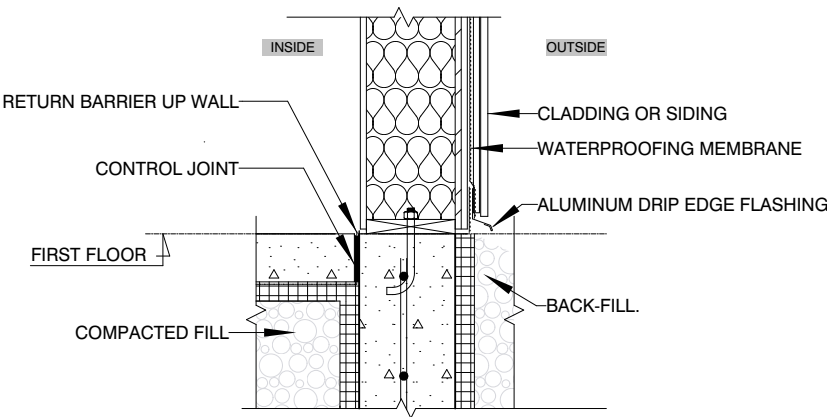


A04-02. 2- FOUNDATION SLAB SECTION

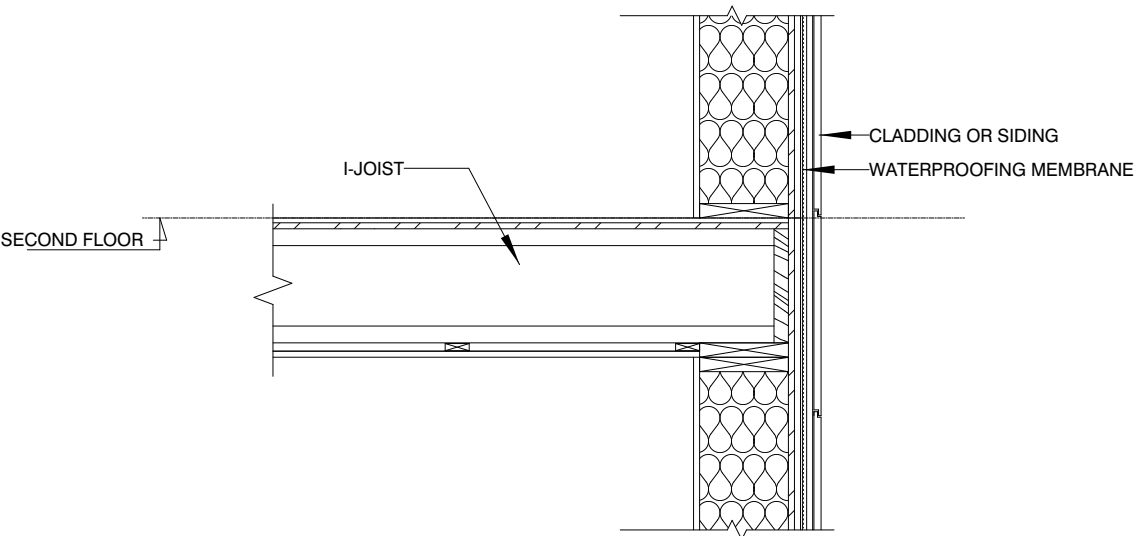

A04-02. 3- FLOOR SECTION

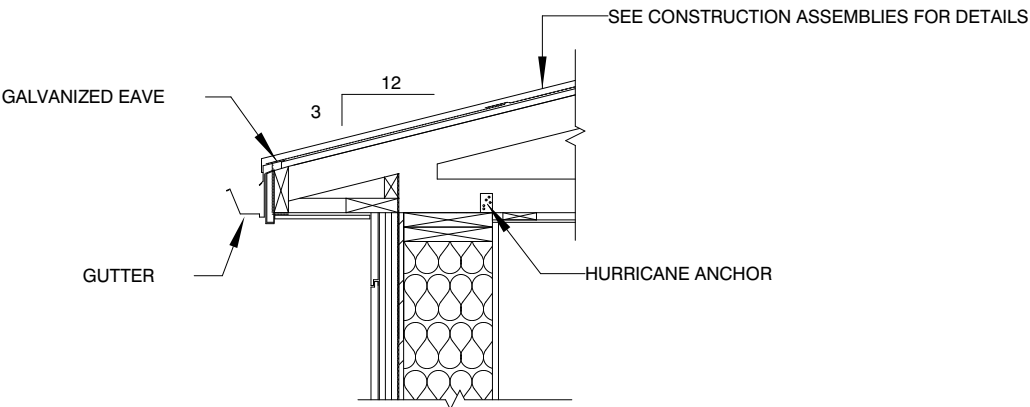

A04-02. 4- SOFFIT DETAILS

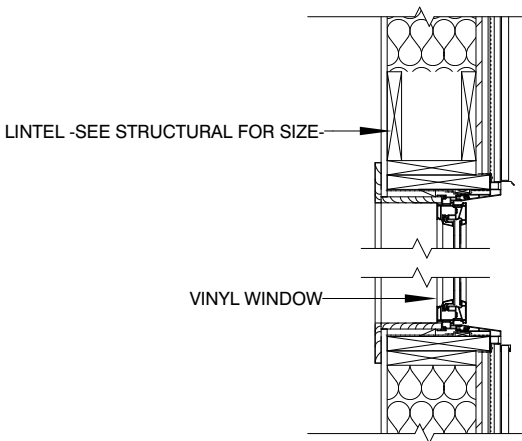

A04-02. 5- VINYL WINDOW DETAILS

Revision History			
RevID	ChID	Change Name	Date
01.	S.A	ISSUED FOR PERMIT	12 DEC.2025




inHabit
Projects + Design

inHabitPD@gmail.com
Halifax, NS


SOI TRADE INC - WALID SALLAM
WAREHOUSE EXTENSION

9 ALICIA SCOTT AVE.
MOUNT UNIACKE, NS
Canada
B0N 1Z0


Drawing Name	
DETAILS (1)	
Drawing Status	
ISSUED FOR PERMIT	
Modified by	Date
SA	Oct 23, 2025
Checked by	Date
BC	Oct 23, 2025
Drawing Scale	
1:20	
Layout ID	Revision
A.04.2	

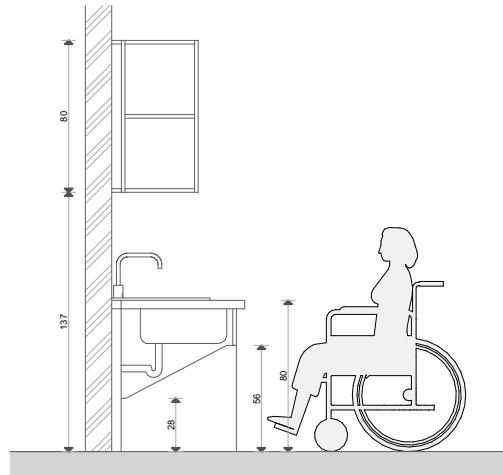


A04-03. 1- B.F SINK DETAILS

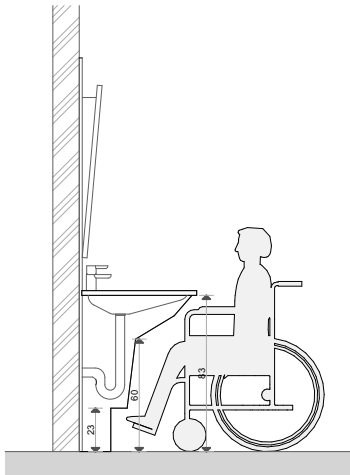

A04-03. 1- B.F VANITY DETAILS

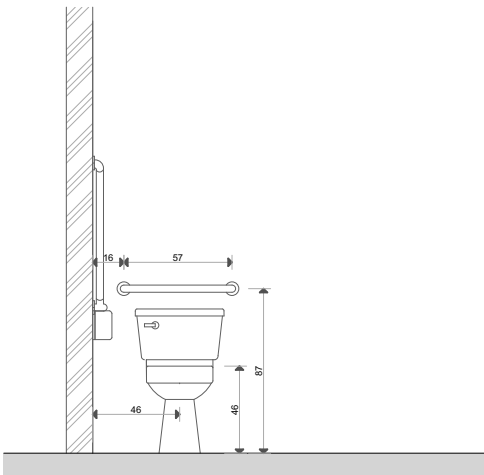

A04-03. 3- B.F WASHROOM FIXTURE

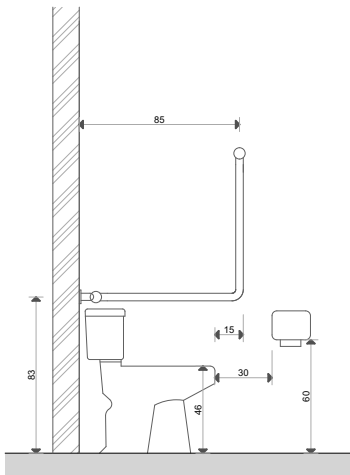

Revision History			
RevID	ChID	Change Name	Date
01.	S.A	ISSUED FOR PERMIT	12 DEC.2025



inHabit
Projects + Design

inHabitPD@gmail.com
Halifax, NS

SOI TRADE INC - WALID SALLAM
WAREHOUSE EXTENSION

9 ALICIA SCOTT AVE.
MOUNT UNIACKE, NS
Canada
B0N 1Z0

Drawing Name
MILLWORK DETAILS

Drawing Status
ISSUED FOR PERMIT

Modified by
SA

Date
Oct 23, 2025





Checked by
BC












Date
Oct 23, 2025

Drawing Scale
1:40

Layout ID
A.04.3

Revision

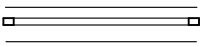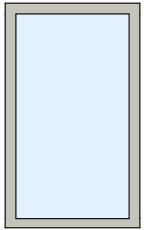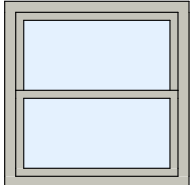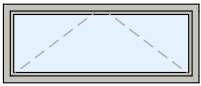WINDOWS			
ELEMENT ID	W-01	W-02	W-03
NAME	Window 24	Window 24	Window 24
QUANTITY	4	6	4
Dim. L x H	91×152	122×122	142×57
2D PLAN			
VIEW			
FIRE RESISTANCE	1h	1h	1h
Thermal transmittance	1.4W/m2K	1.4W/m2K	1.4W/m2K
Acoustic transmission class	25	25	25

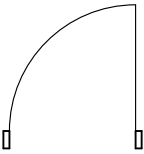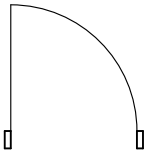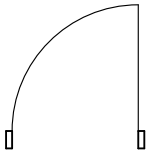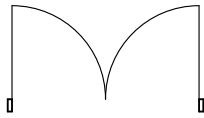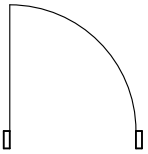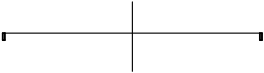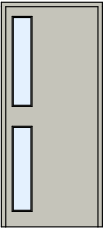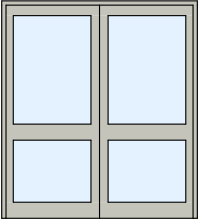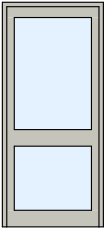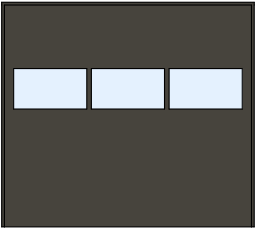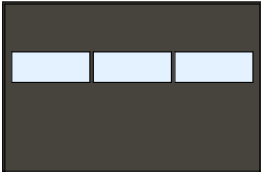DOORS							
ID ELEMENET	D01	D02	D03	D03	D04	GD01	GD02
NAME	Door 24	Door 24	Door 24	Double Door 24	Door 24	Vertical Sliding Garage Do...	Vertical Sliding Garage Doo...
QUANTITY	4	4	1	1	2	3	1
Dim. L x H	91×203	91×203	91×203	183×203	91×203	274×244	373×244
2D PLAN							
VIEW							
Fire resistance index	1h	1h	1h	1h	1h	30 minutes	30 minutes
Thermal transmittance	1.4W/m2K	1.4W/m2K	1.4W/m2K	1.4W/m2K	1.4W/m2K	1.4W/m2K	1.4W/m2K
ACOUSTIC TRANSMISSION CLASS	25	25	25	25	25	25	25
Emergency door	☐	☐	☐	☒	☒	☐	☐
Accessibility door	☐	☒	☒	☒	☒	☐	☐
Sound Reduction	Yes	Yes	Yes	Yes	Yes	Yes	Yes
Composite	☒	☒	☒	☐	☐	☐	☐
Core type	Solid core	Solid core	Solid core	Alum+Glaz	Alum+Glaz	Insulated with 3" Neufoam	Insulated with 3" Neufoam

Revision History			
RevID	ChID	Change Name	Date
01.	S.A	ISSUED FOR PERMIT	12 DEC.2025



inHabit
Projects + Design

inHabitPD@gmail.com
Halifax, NS

SOI TRADE INC - WALID SALLAM
WAREHOUSE EXTENSION

9 ALICIA SCOTT AVE.
MOUNT UNIACKE, NS
Canada
B0N 1Z0

Drawing Name

Schedueles: Windows, Doors

Drawing Status

ISSUED FOR PERMIT

Modified by

SA

Date

Oct 23, 2025

Checked by

BC

Date

Oct 23, 2025

Drawing Scale

1:1

Layout ID

A.05.1

Revision

PERSPECTIVE 01



PERSPECTIVE 02



Revision History			
RevID	ChID	Change Name	Date
01.	S.A	ISSUED FOR PERMIT	12 DEC.2025



inHabit
Projects + Design

inHabitPD@gmail.com
Halifax, NS

SOI TRADE INC - WALID SALLAM
WAREHOUSE EXTENSION

9 ALICIA SCOTT AVE.
MOUNT UNIACKE, NS
Canada
B0N 1Z0

Drawing Name	
PERSPECTIVES	
Drawing Status	
ISSUED FOR PERMIT	
Modified by	Date
SA	Oct 23, 2025
Checked by	Date
BC	Oct 23, 2025
Drawing Scale	
Layout ID	Revision
A.06.1	